

B E Y Z A   G Ö R E N

P O R T F O L I O

# B E Y Z A G Ö R E N

05 January 1999

## Education

2023 - 2025

**Politecnico di Milano** Milan, Italy

School of Urban Planning Construction Engineering  
Master's Degree, Architecture - Building Architecture

2017 - 2021


**Istanbul Kultur University** Istanbul, Türkiye

Faculty of Architecture  
Bachelor's Degree, Architecture

## Skills

## Programs

ArchCAD  
Revit  
AutoCAD  
Rhino  
Sketchup  
Adobe Illustrator  
Adobe InDesign  
Adobe Photoshop  
Lumion

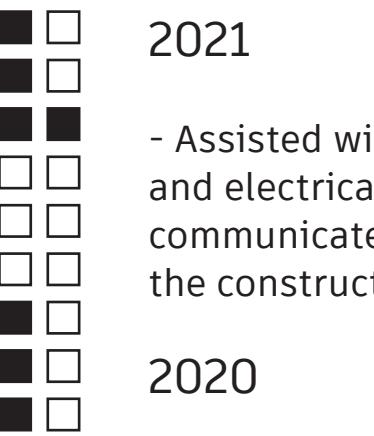

## Languages

**English** (Professional), **German** (B1), **Italian** (A2), **Turkish** (Native)

Viale Andrea Doria 29, Milano Italia  
+49 178 4556877  
gorenbeyzami@gmail.com

## Experiences

2025

**Politecnico di Milano** Milan, Italy

Machine Housing Concept Workshop

- Explored how AI can assist and enhance architectural design processes, focusing on construction systems, materials, and self configurable housing concepts with using sustainable materials from Materiom database.
- Analyzed existing AI tools and collaborated with AI rendering tools in order to visualise the experimental sustainable materials in real life.
- In workshop; paper composite, coffee grounds, agar agar and cotton fibers are used as an architectural material.

2021 - 2022

**Multi Corporation** Istanbul, Türkiye

Junior Architect in Leasing Department

- Maintaining good tenant/investor relations by utilizing professional communication and take the necessary steps to resolve situations happened in the malls.
- Examined the design requests of the tenants for the premises, which the requests are convenient to the general mall concept or not. Negotiated over proposed design ideas to develop architecturally.

2021

**Eksen Architecture and Engineering** Istanbul, Türkiye

Construction Site Internship, Intern Architect


- Assisted with the production of construction drawings, such as architectural and electrical plans, architectural schedules, and sections. Had the opportunity to communicate accompany firm partners to assorted construction sites to oversee the construction process and discuss progress with workers.

2020

**Dikmen Tayfur Arcitecture** Istanbul, Türkiye


Office Internship, Intern Architect

- Involved in design development phase of skii center, restaurant and hotel projects actively. Working on AutoCAD, Archicad and Revit in these projects.

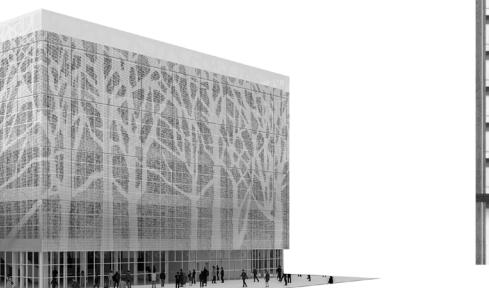

Bosco della Musica

Concert Hall in Milan Rogoredo

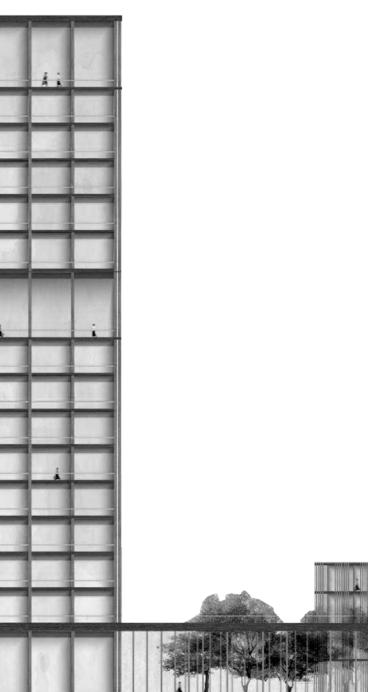

Timber Tall Building

Timber Tall Building in Zurich Hardturm



Cinifabrique



Workshop Space in Milan


Politecnico di Milano

School of Architecture Urban Planning Construction Engineering  
Master of Science Architecture - Building Architecture 2024/2025  
Architectural Design Studio For Complex Constructions 2



Prof. Maria Grazia Folli, Prof. Corrado Pecora, Prof. Marco Imperadori,  
Prof. Giovanni Dotelli, Prof. Luca Sarto

### BOSCO DELLA MUSICA

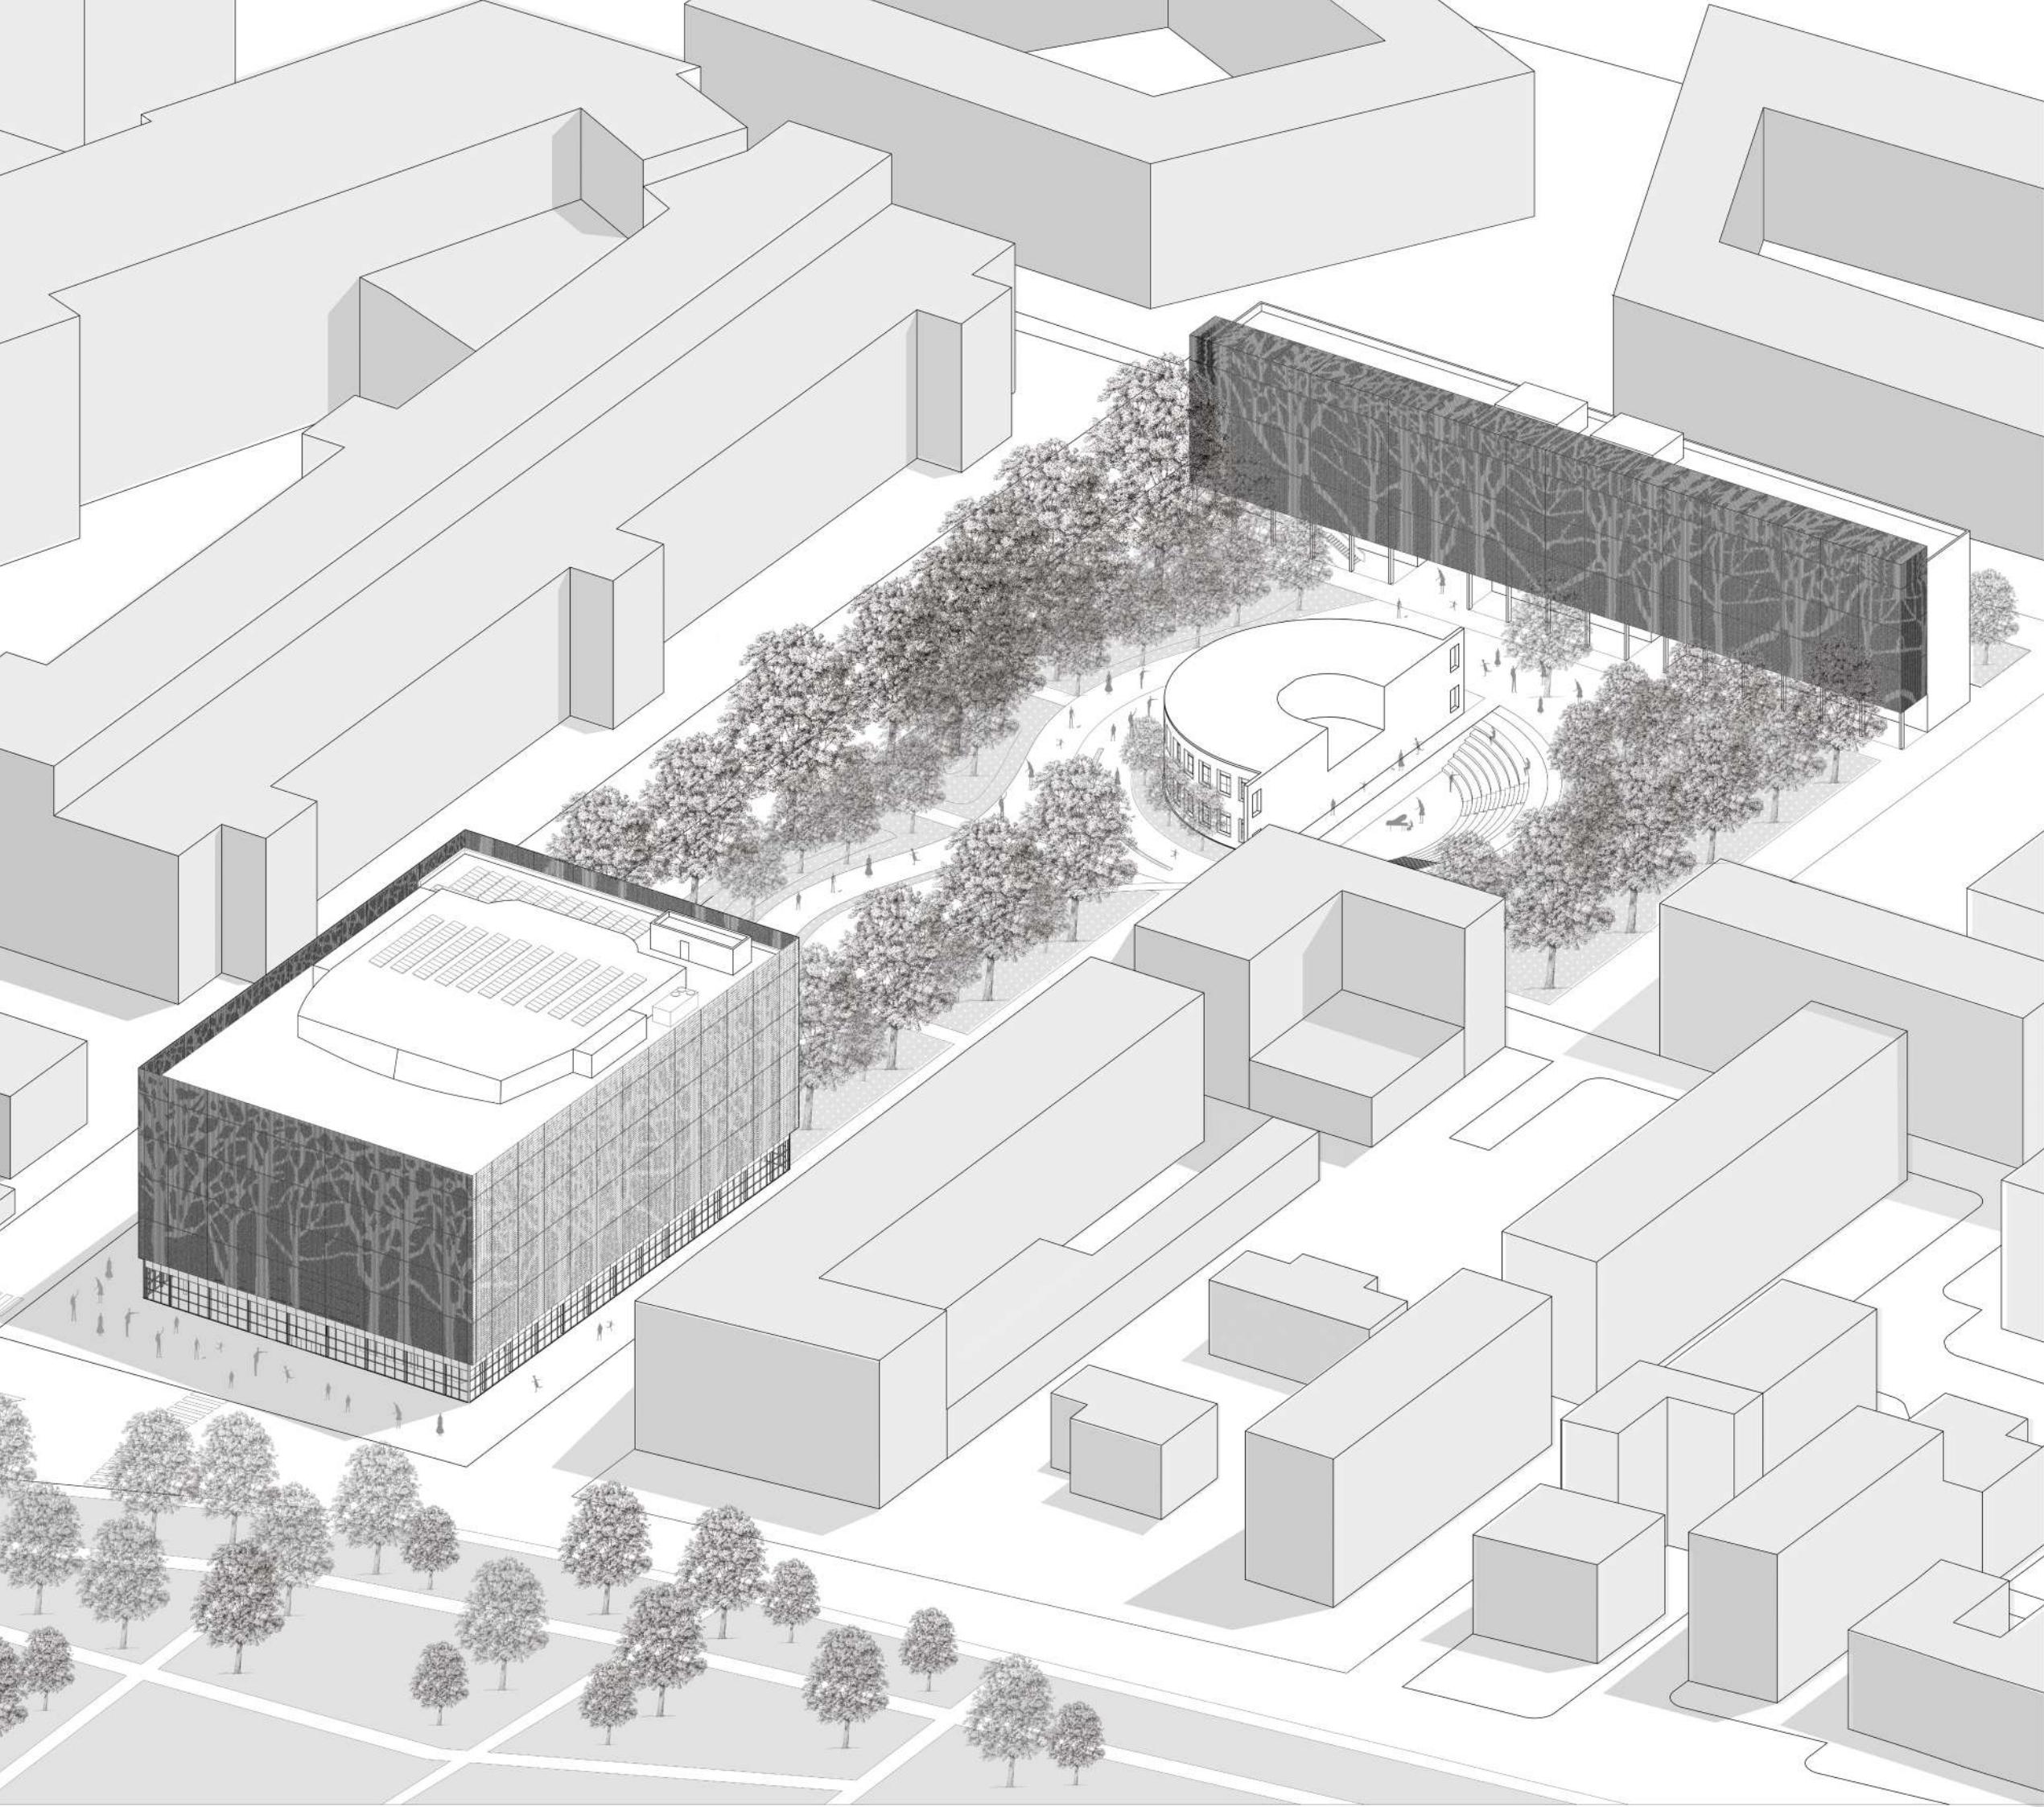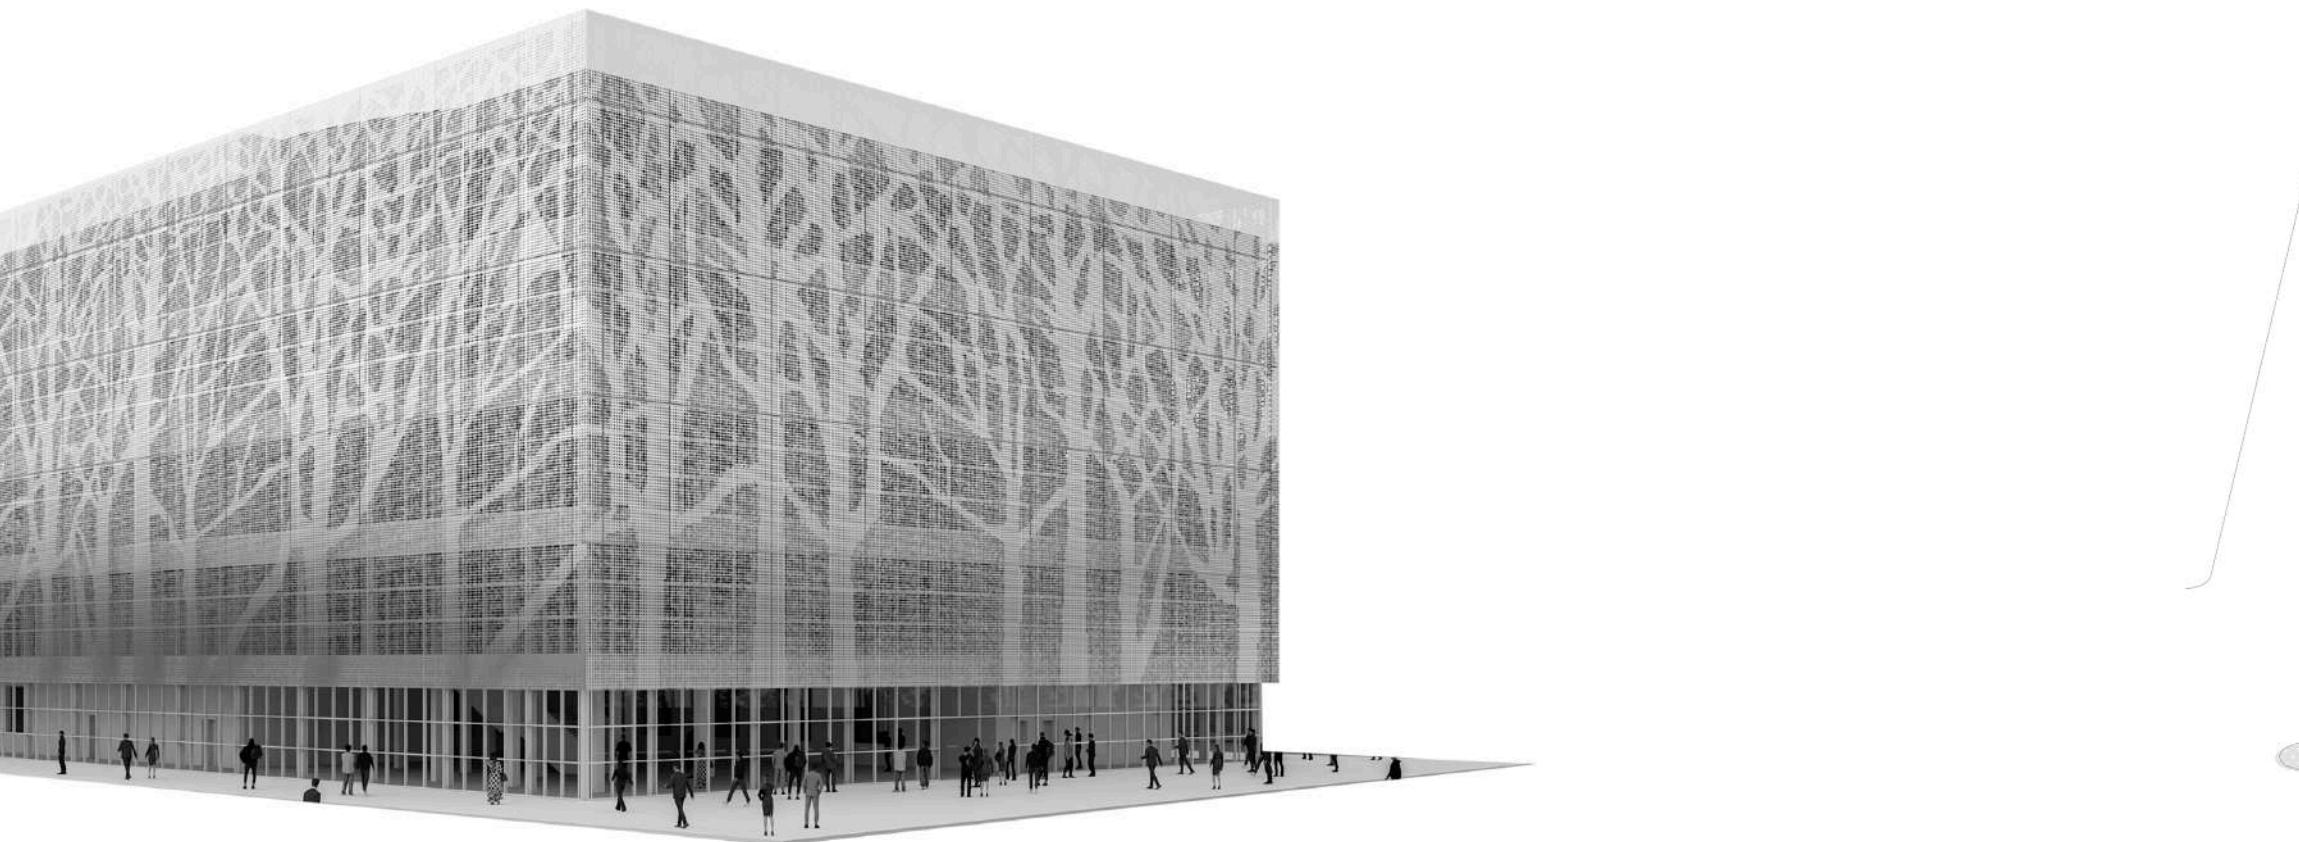

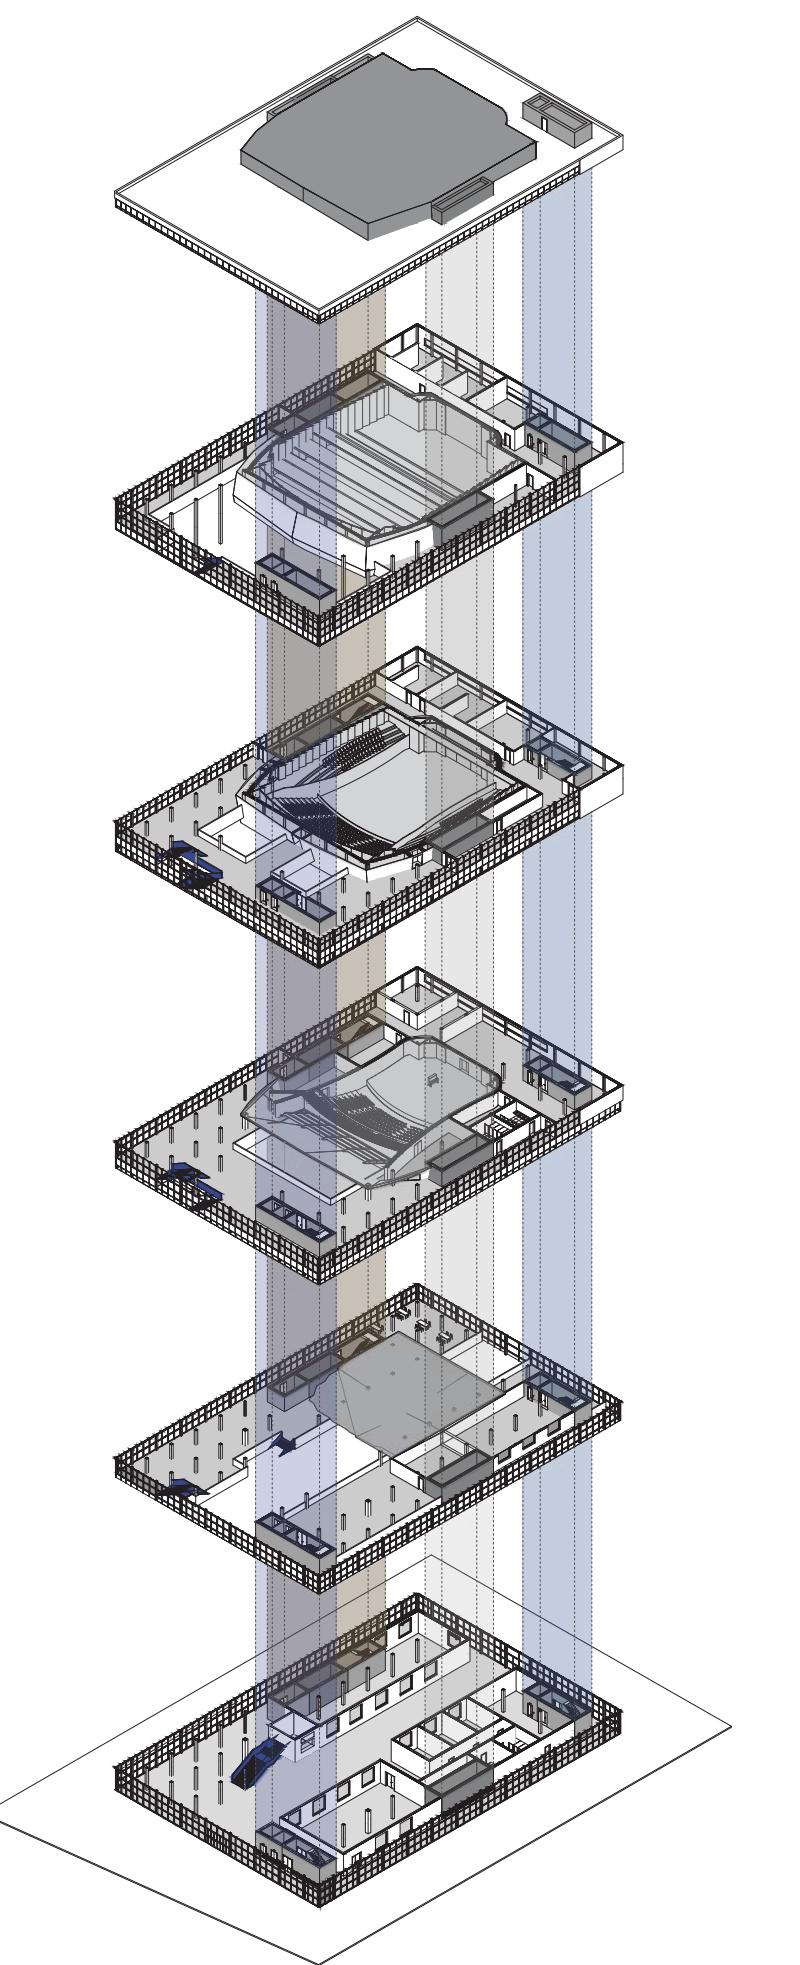


Master Plan

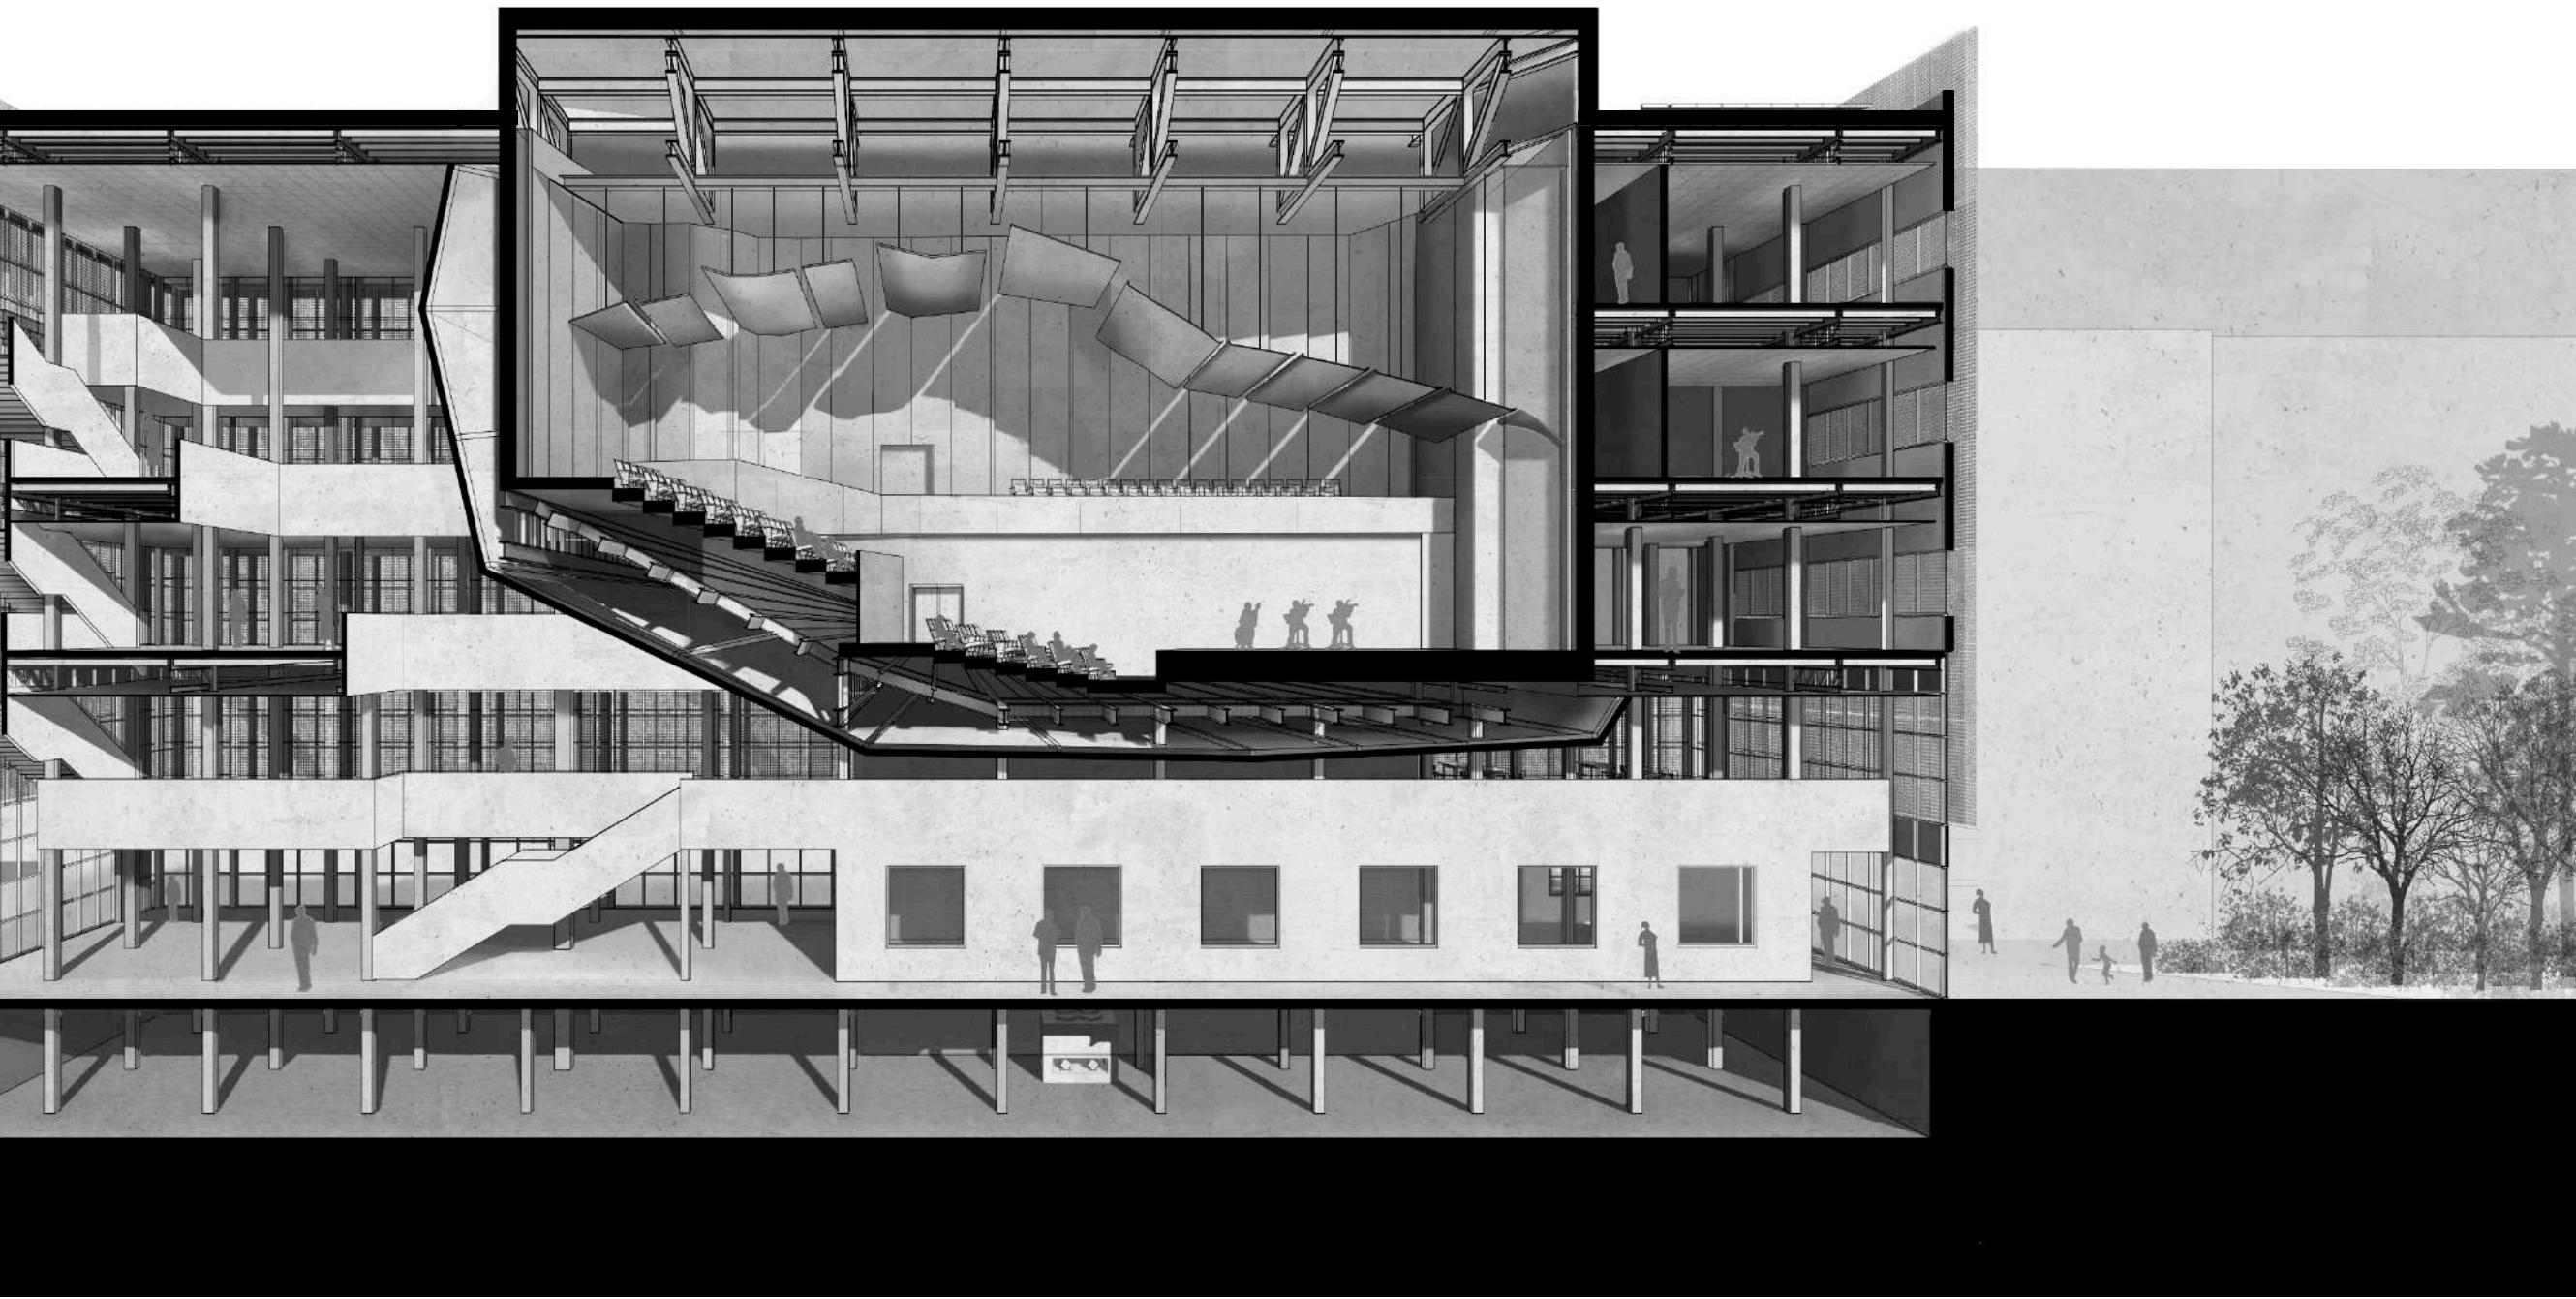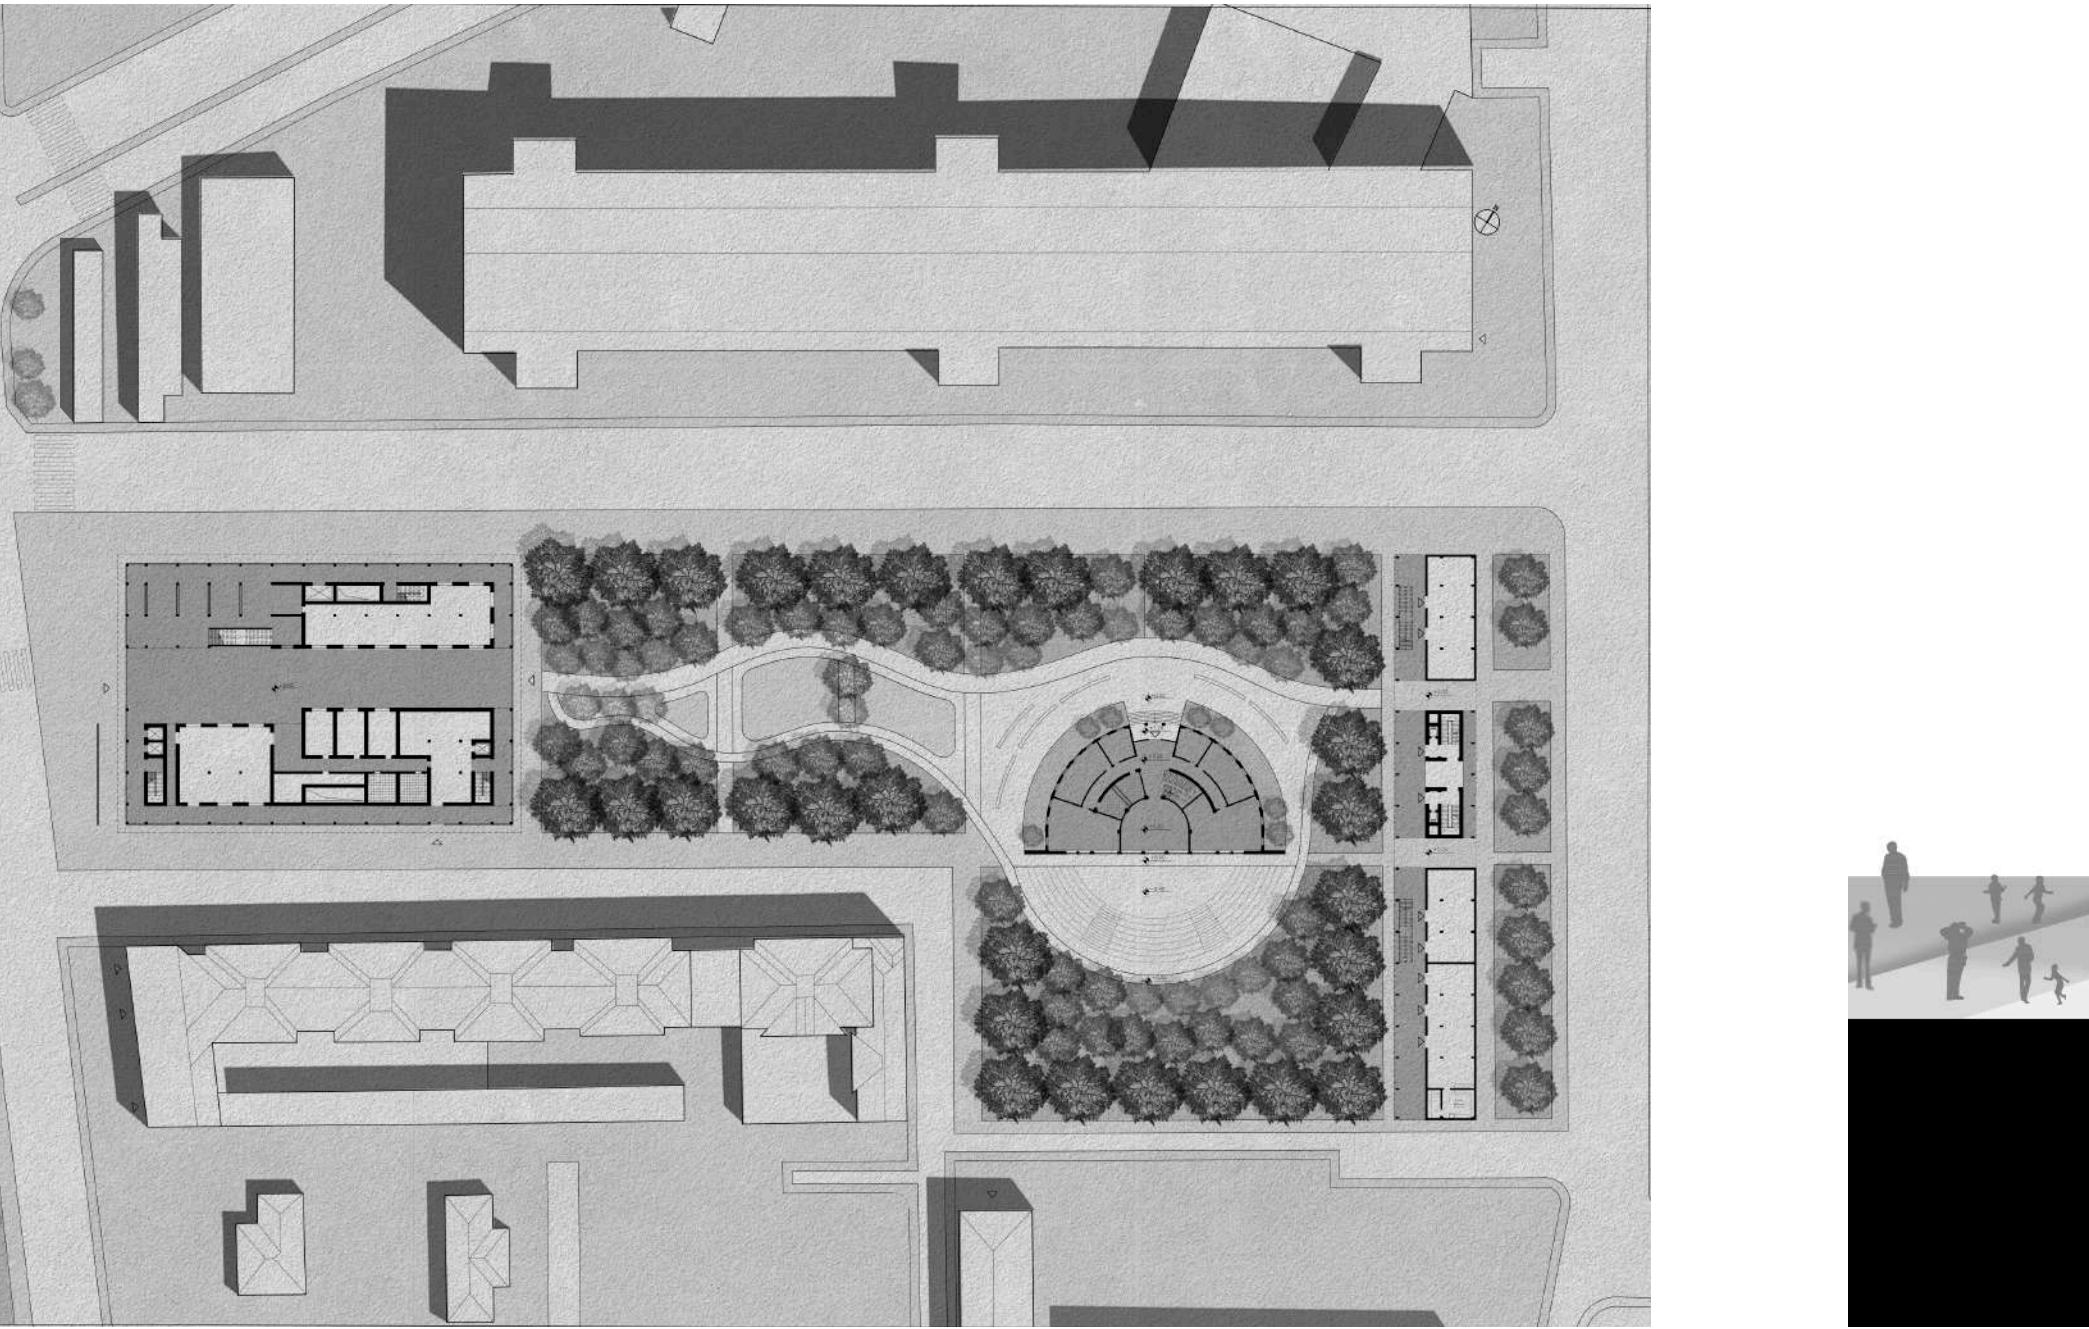





8



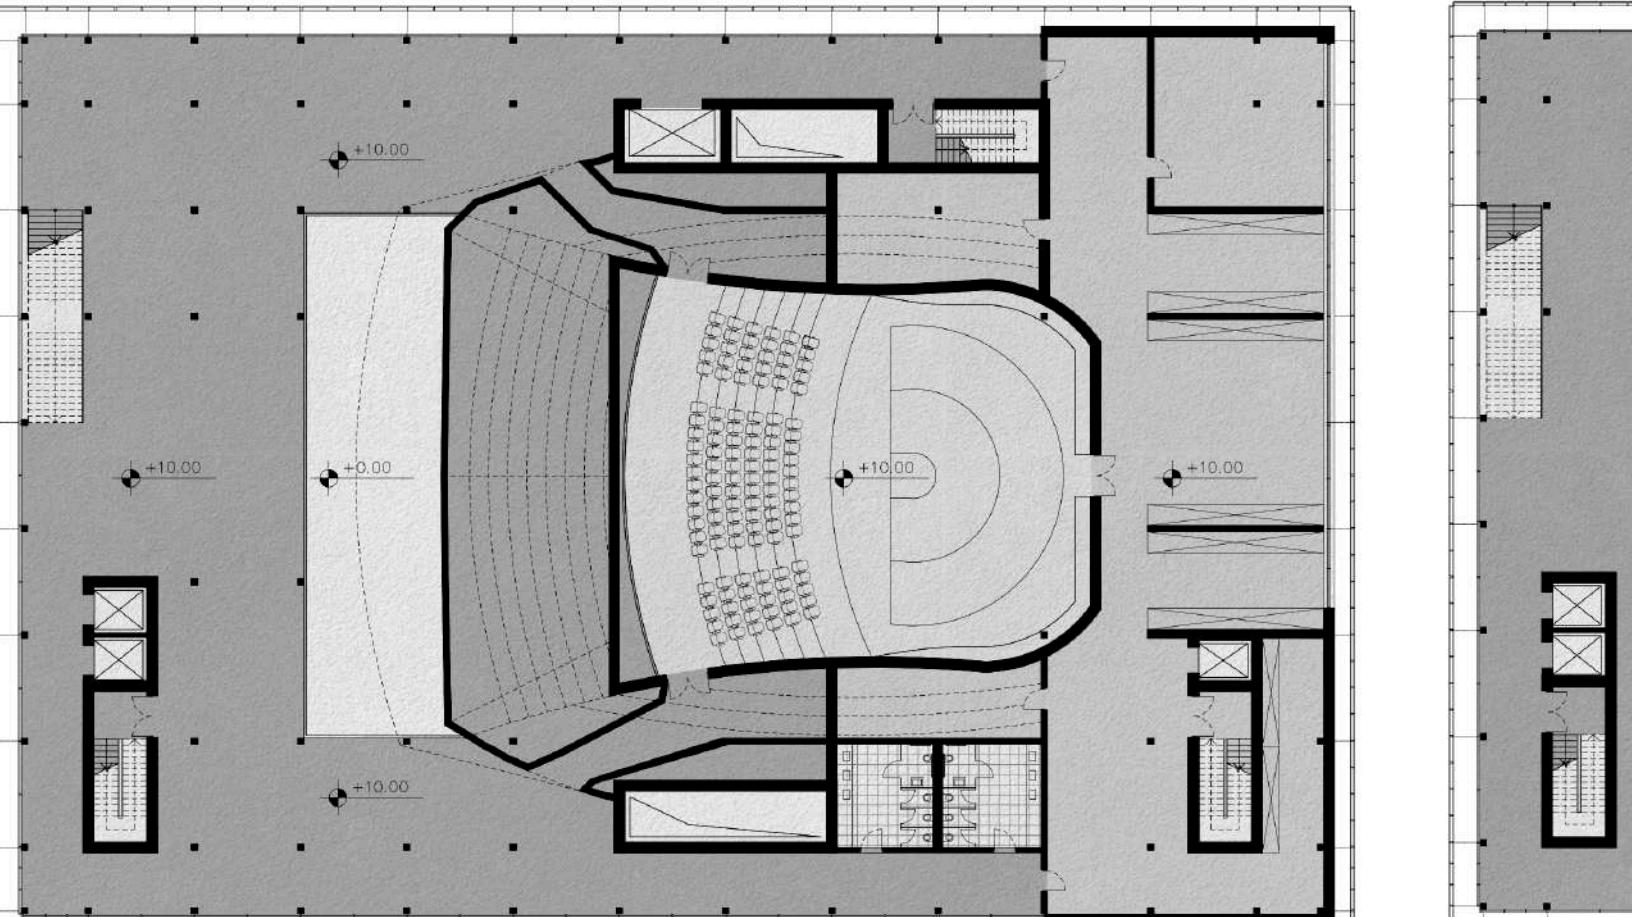


Concert Hall Plan Level I (+10.00)

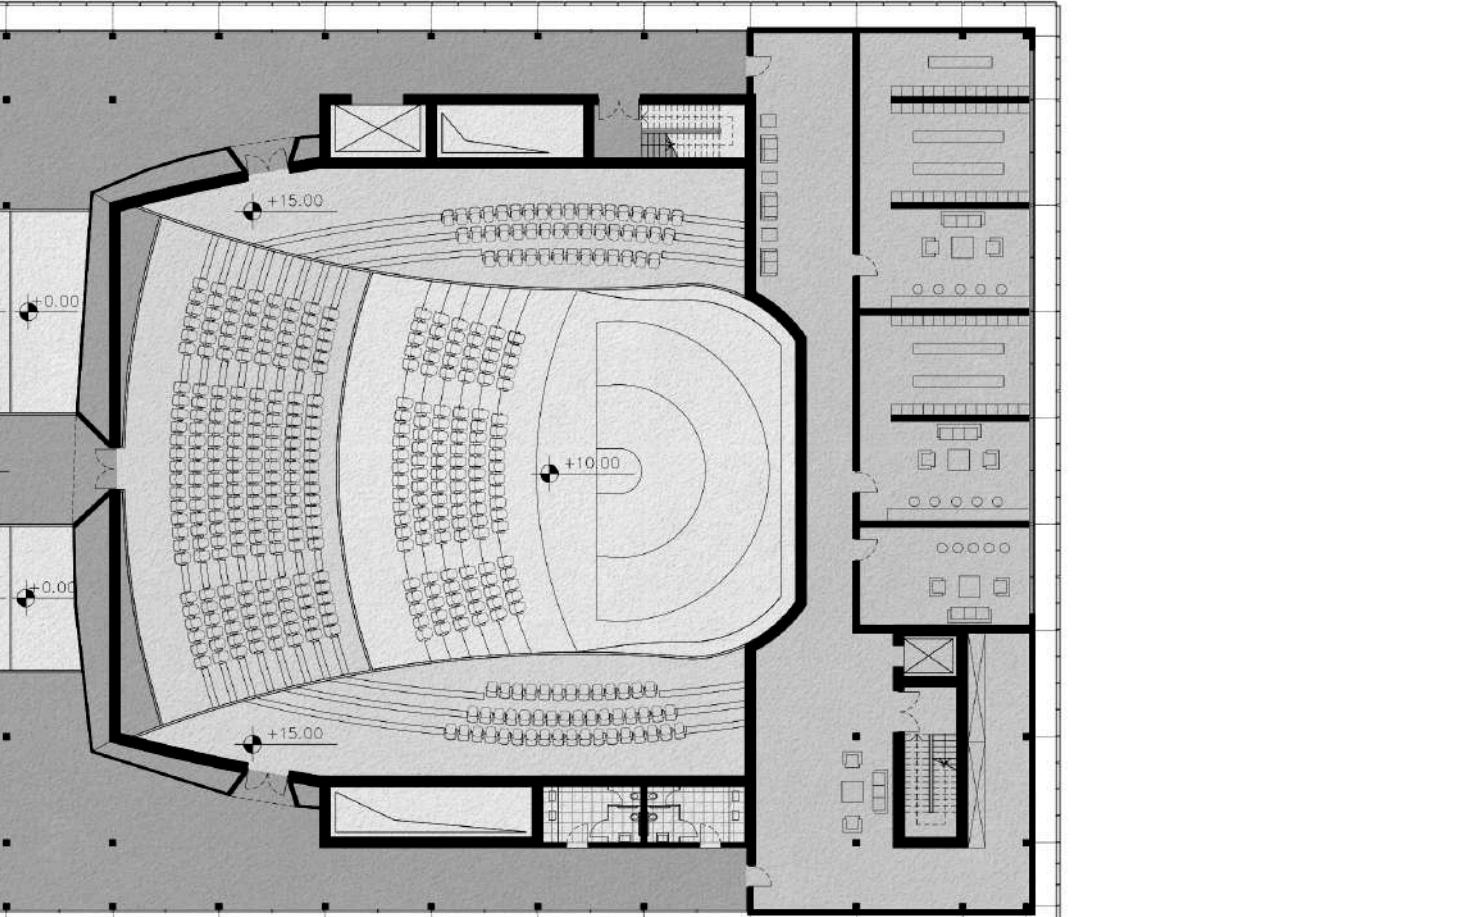

Concert Hall Plan Level II (+15.00)

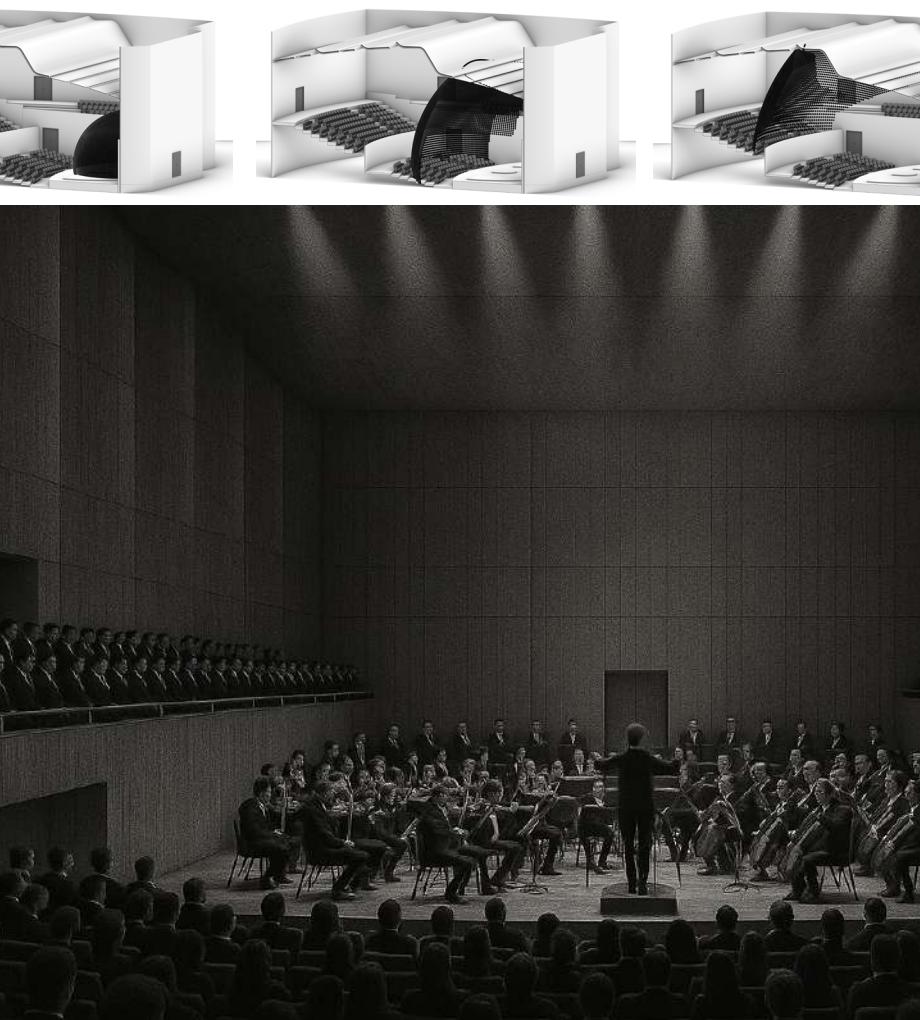

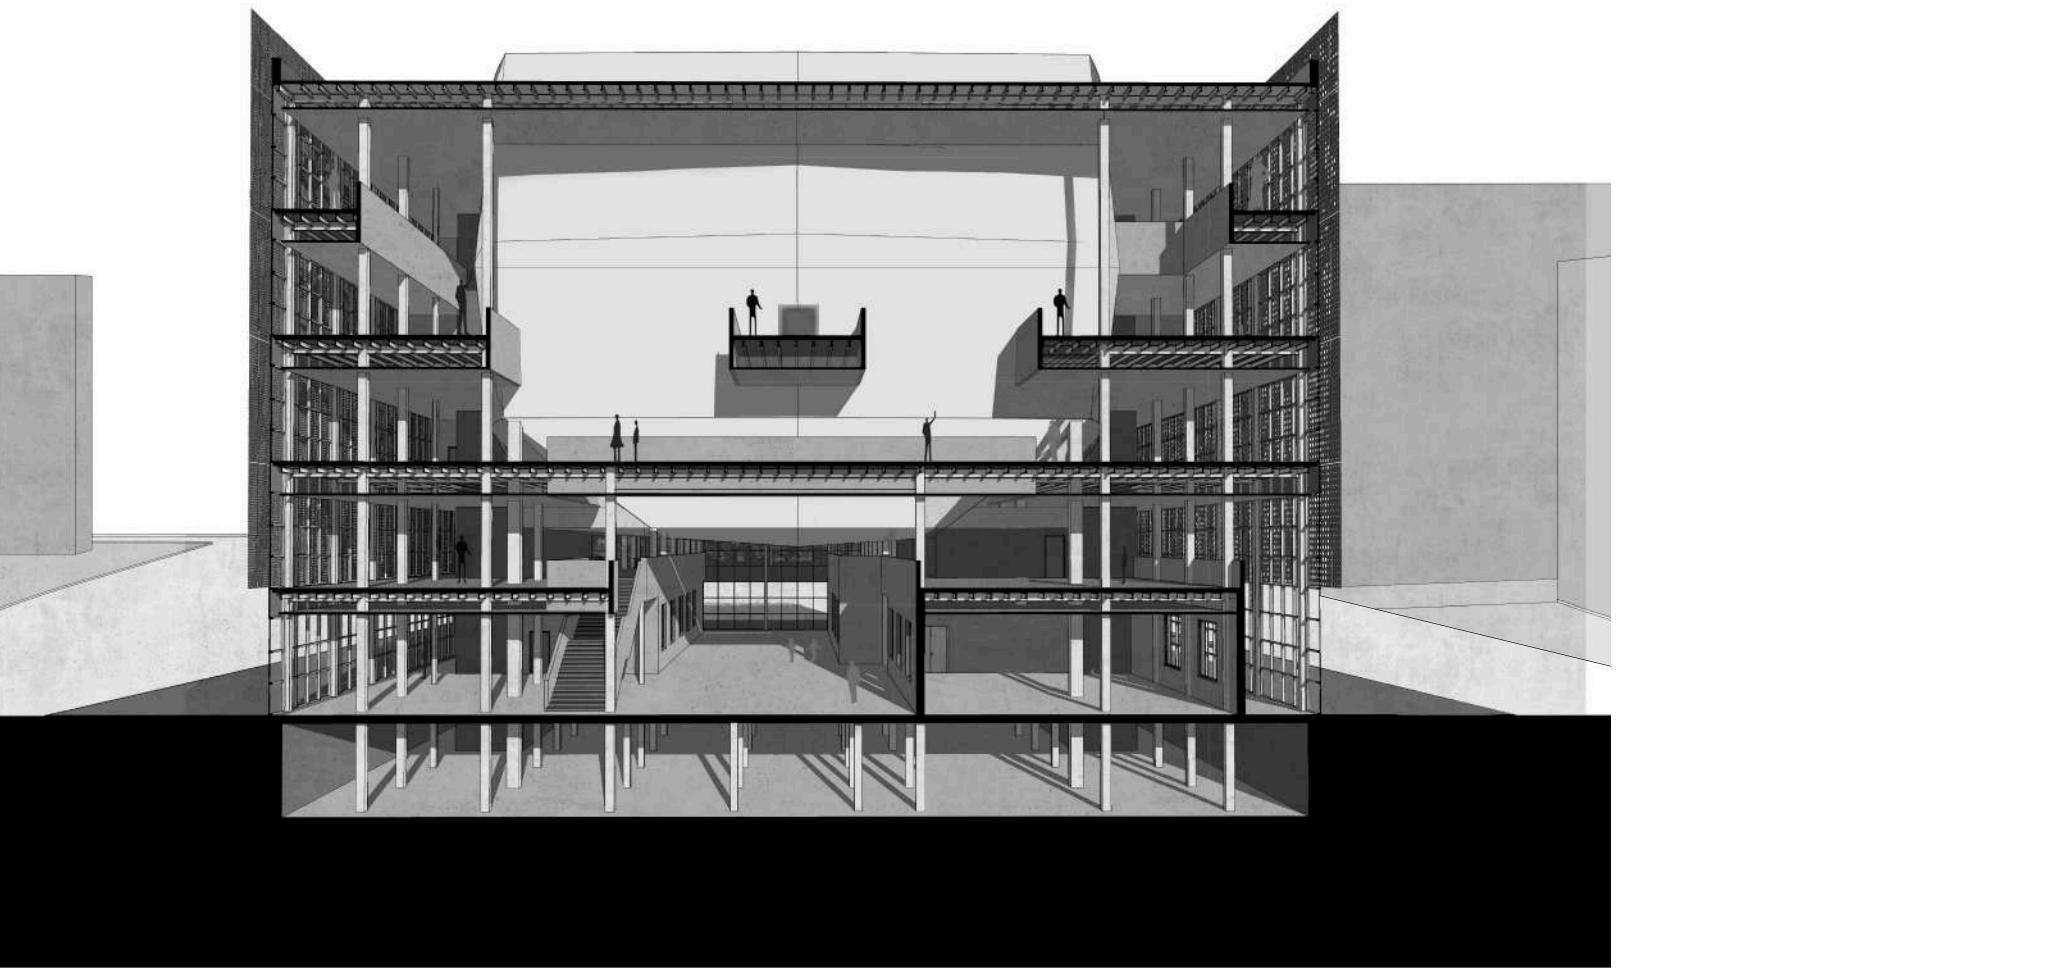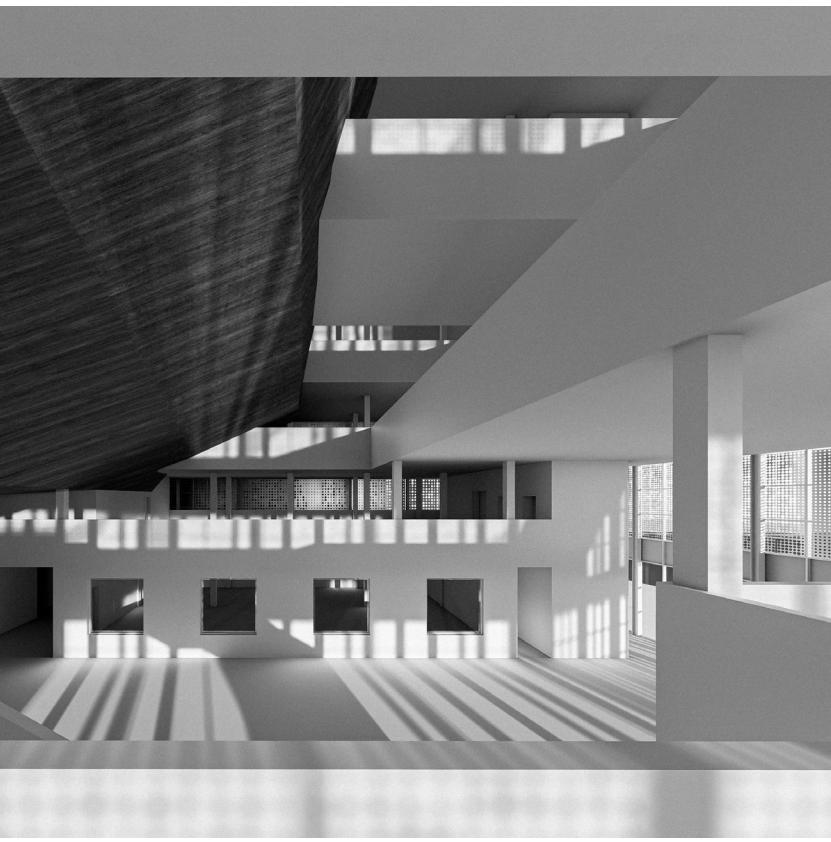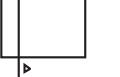
Perspective Section 

Foyer from First Floor Level (+5.00)




Foyer / Passage from Ground Floor Level (+0.00)


Foyer Area Renders

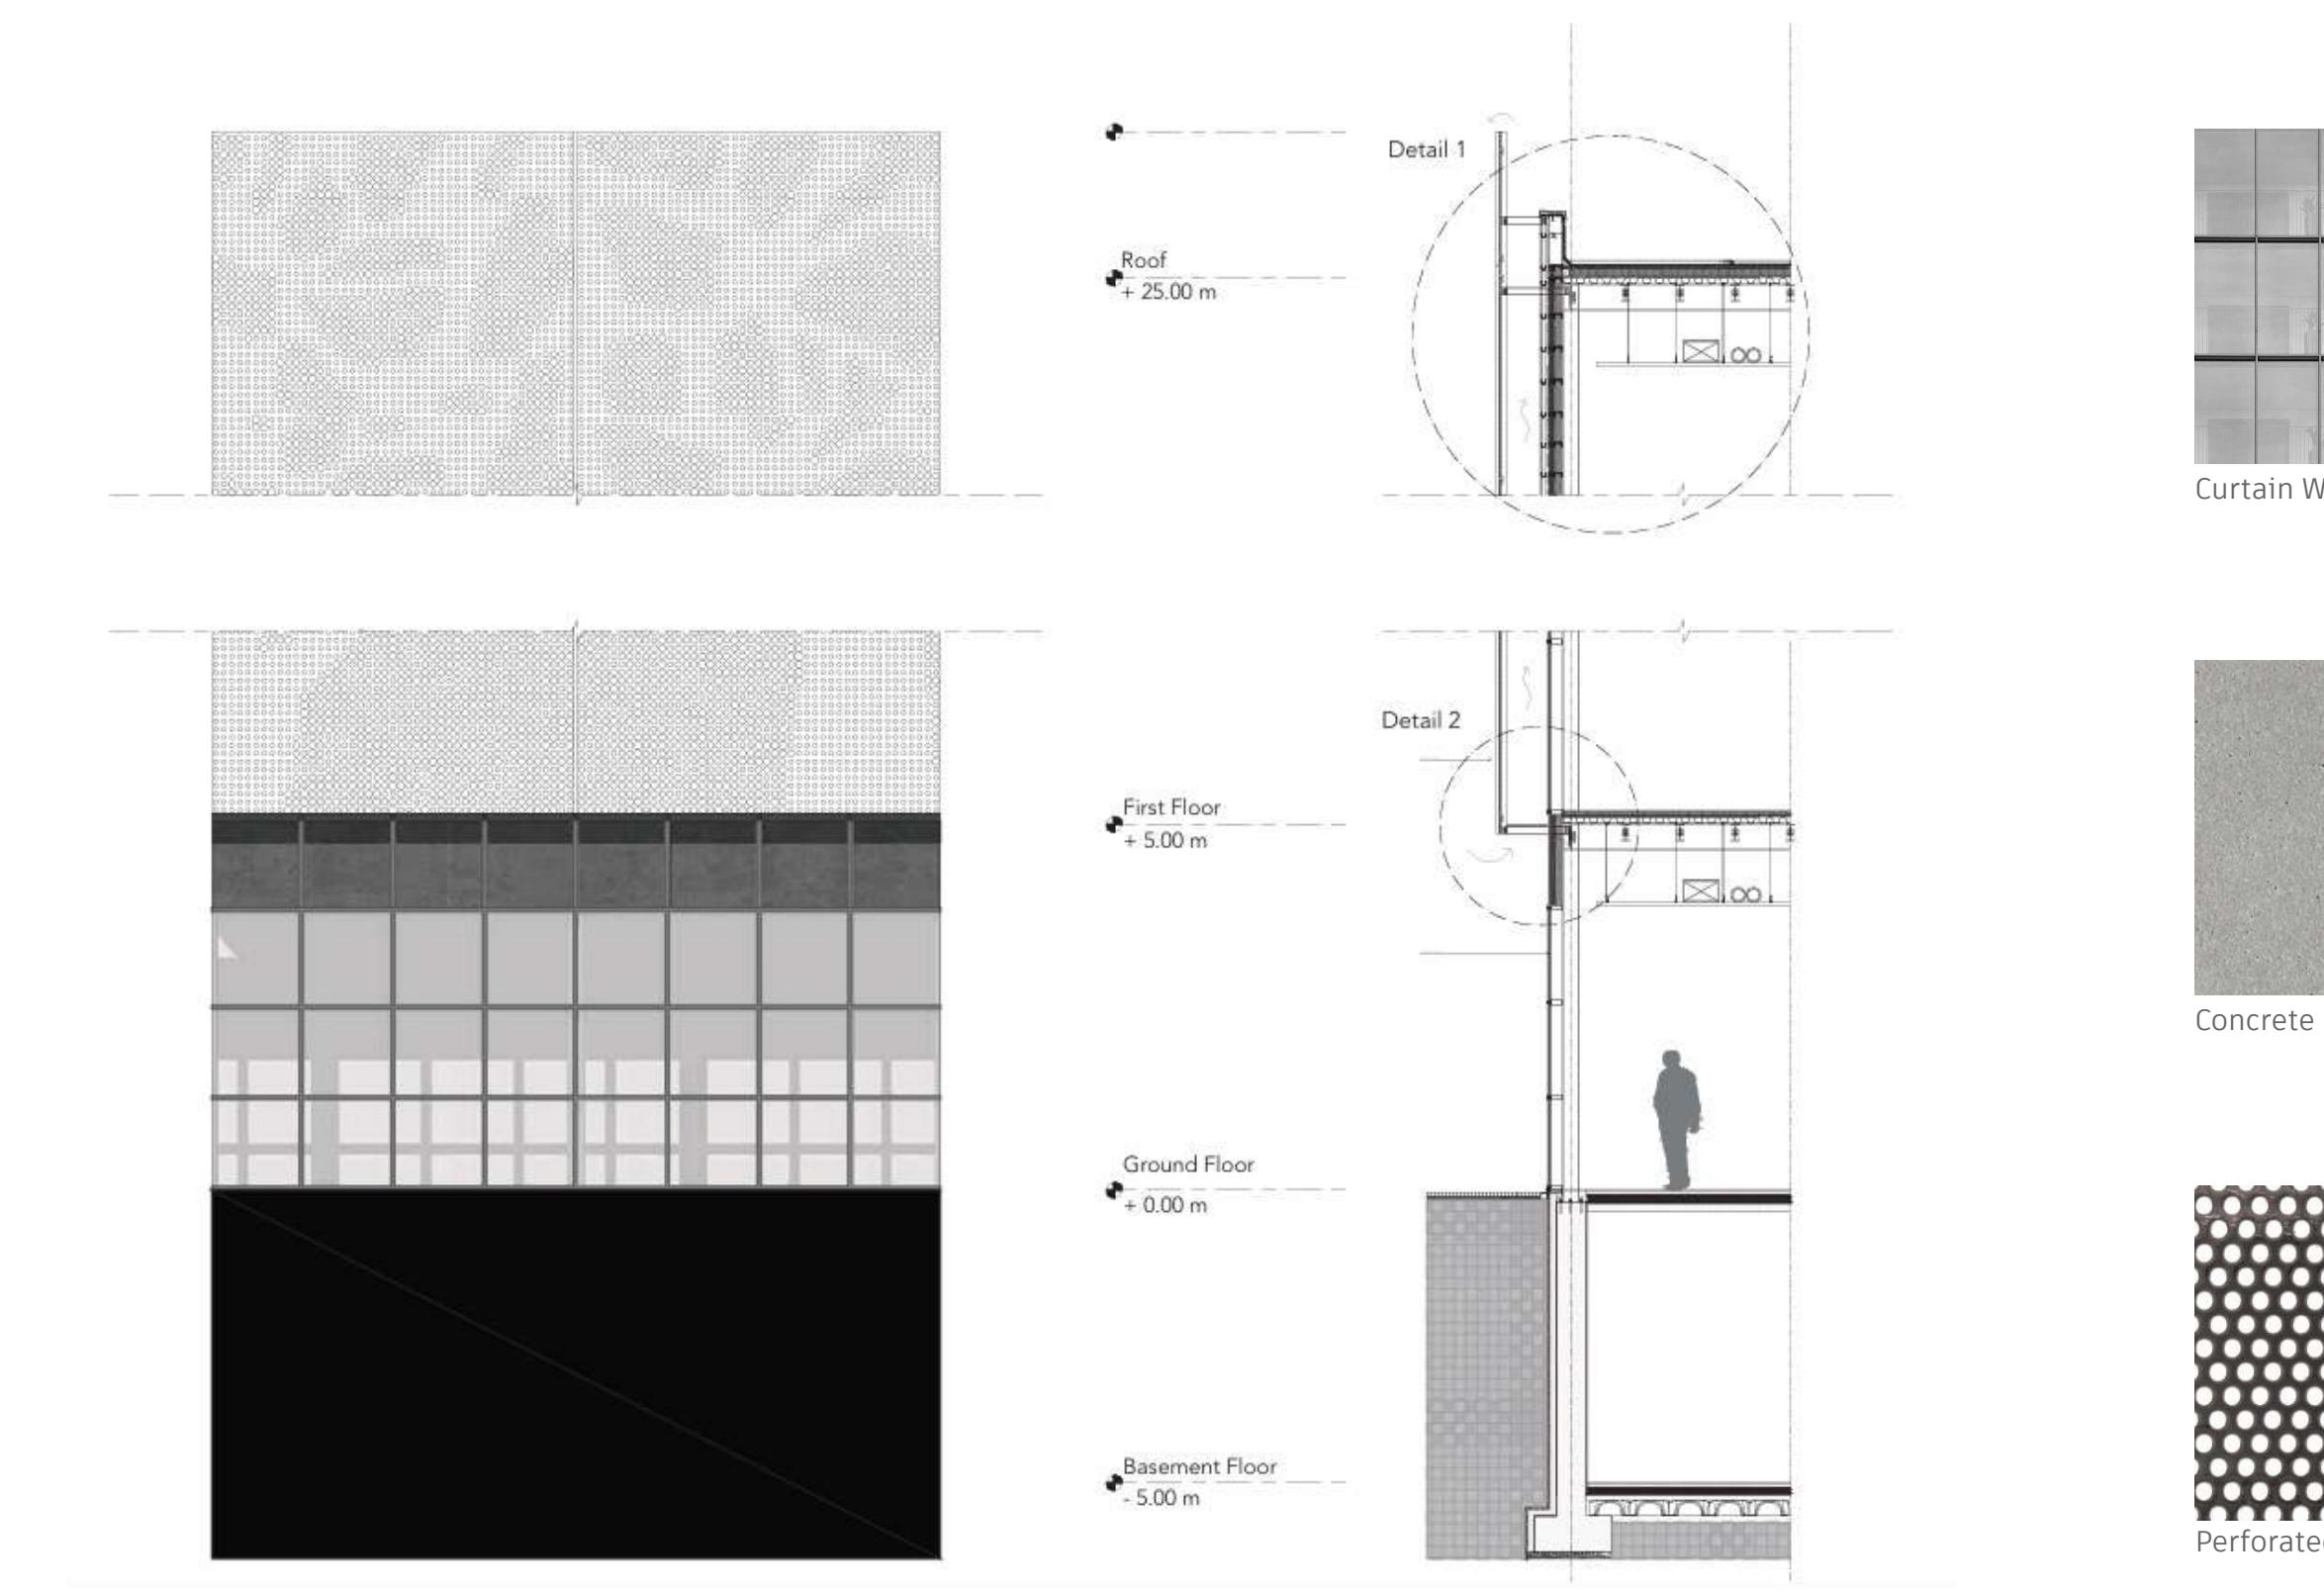


Materiality and Facade Details

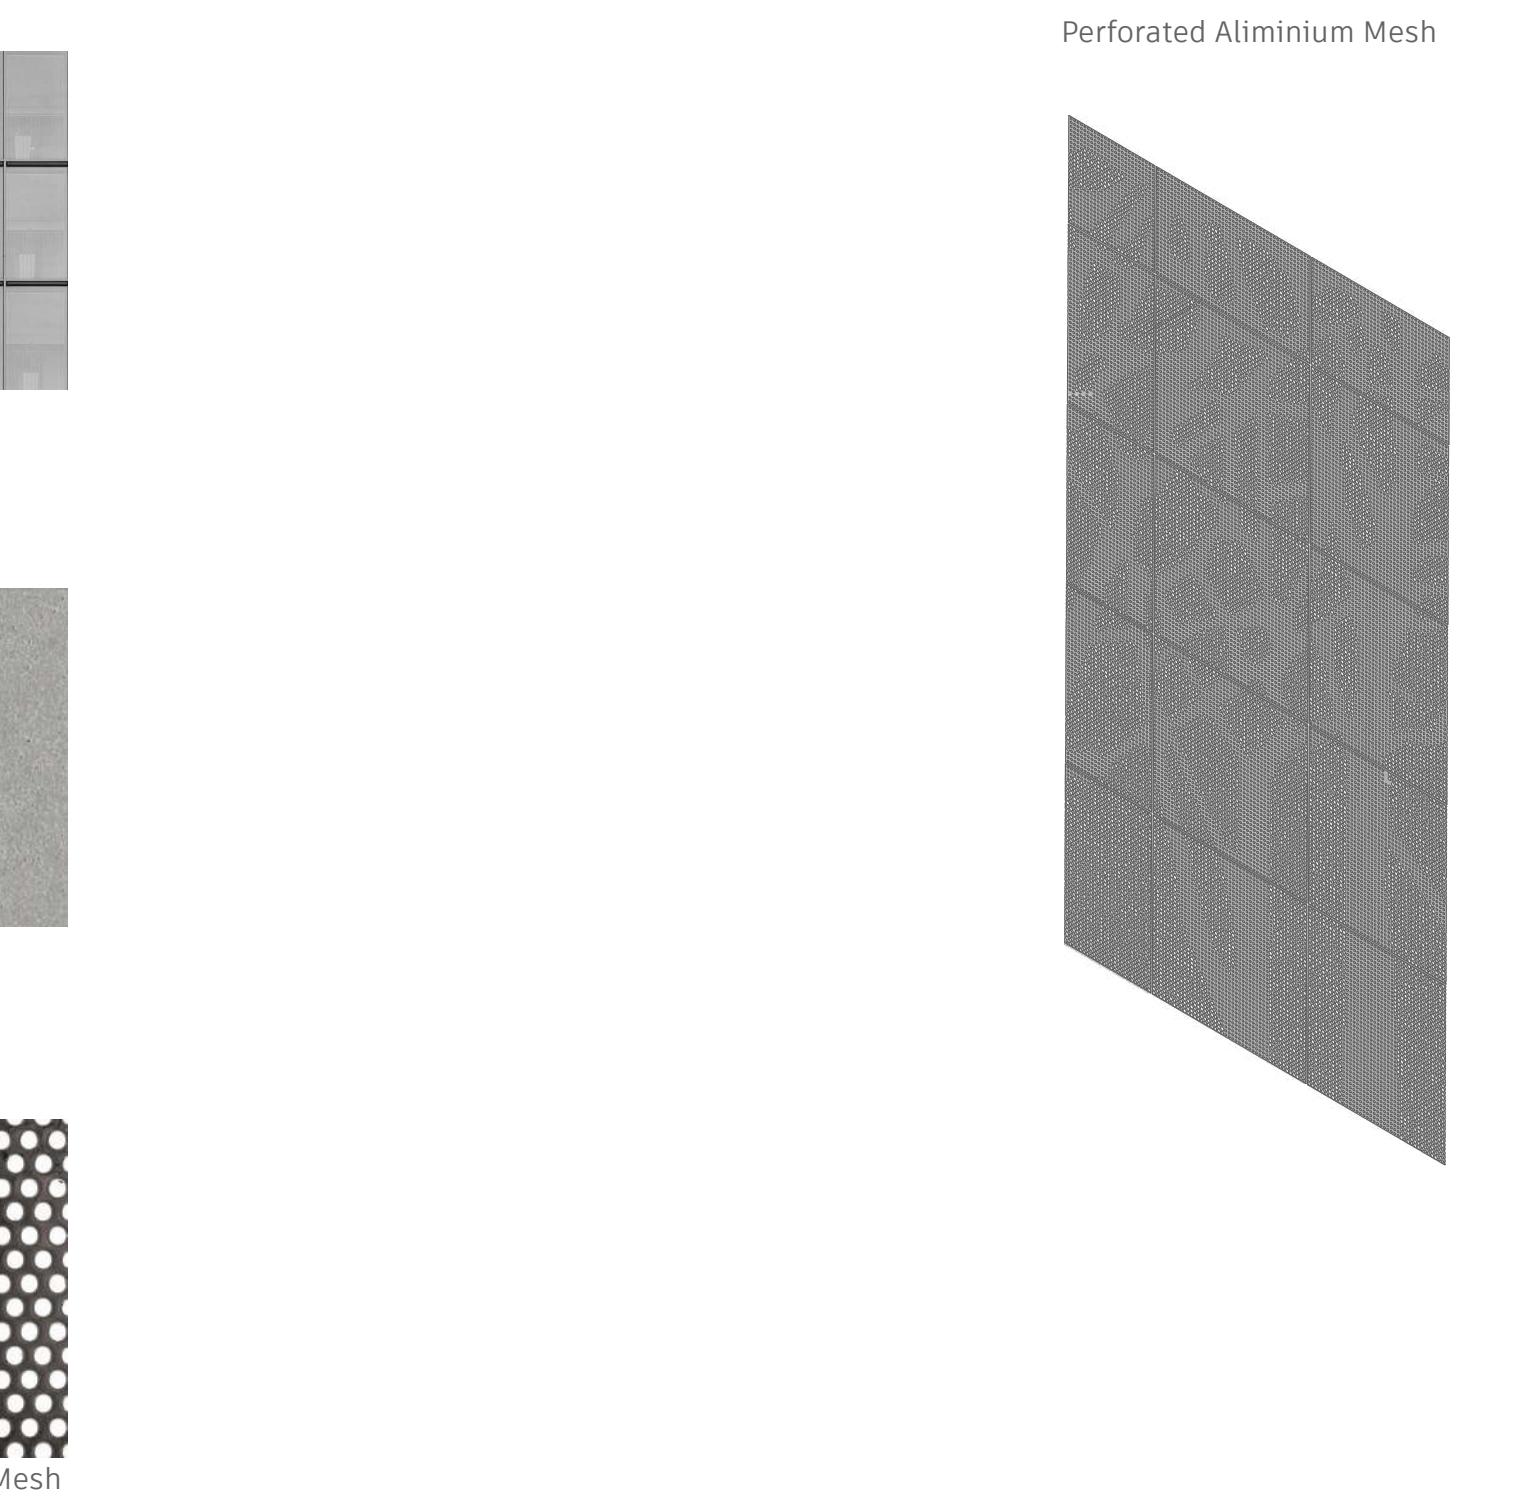


Exploded Axonometry of Facade Design

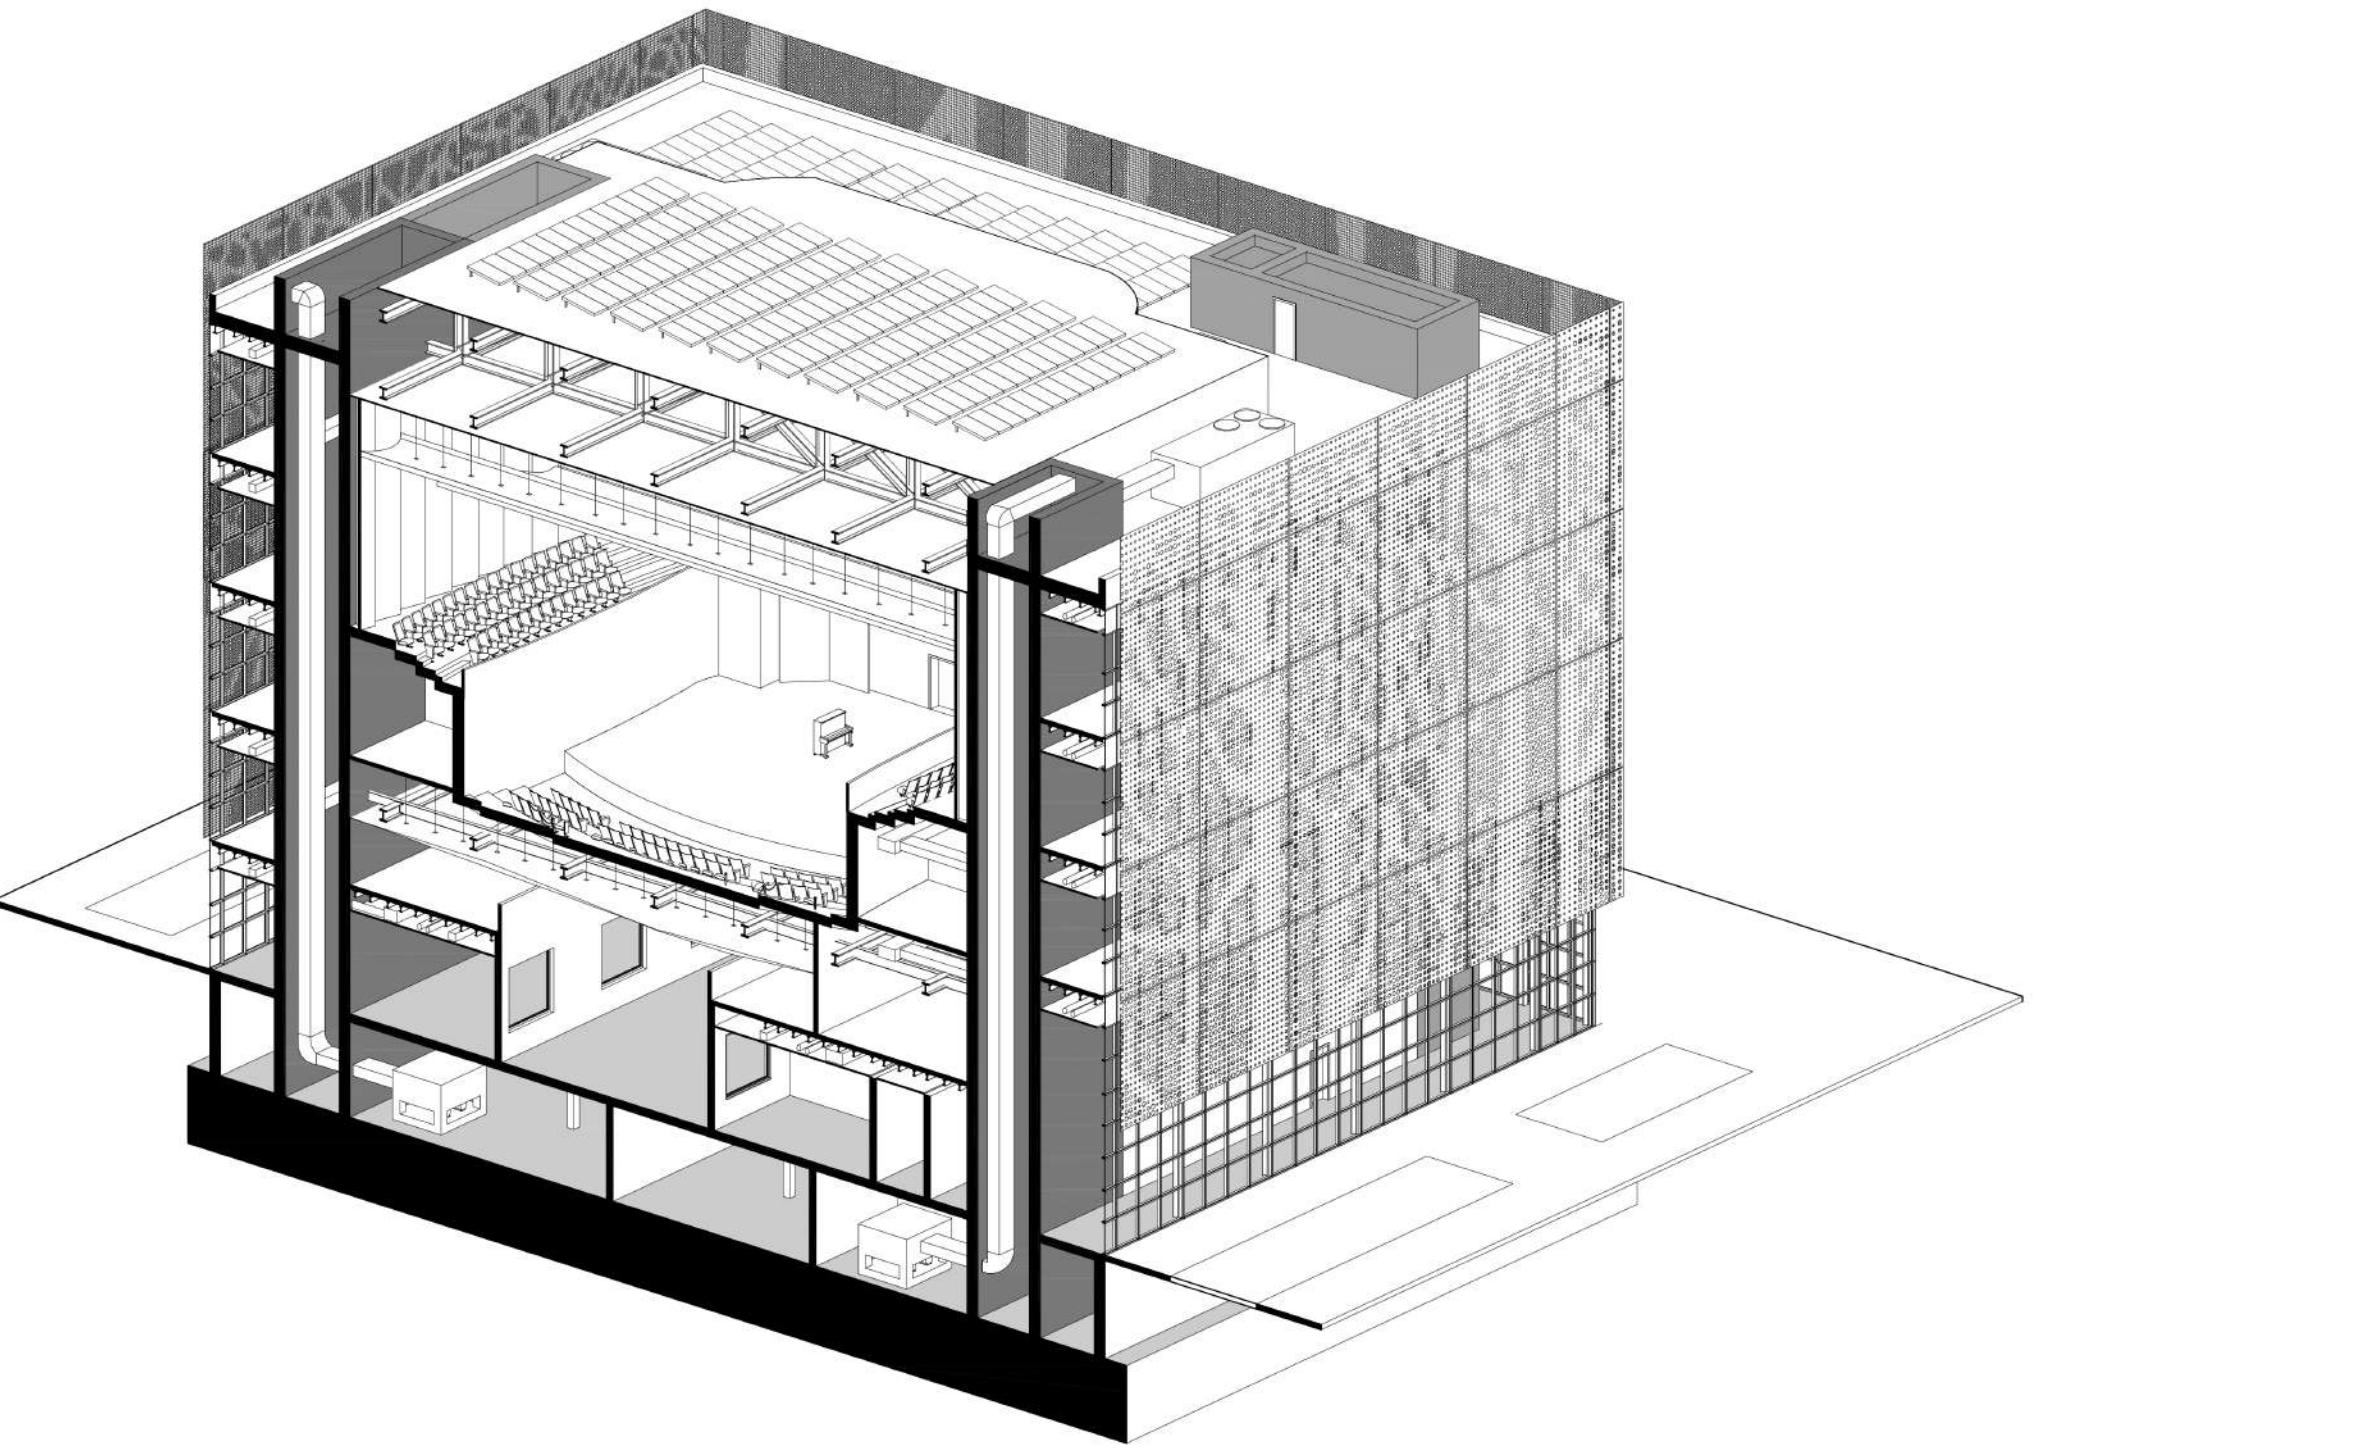

Axonometric Section

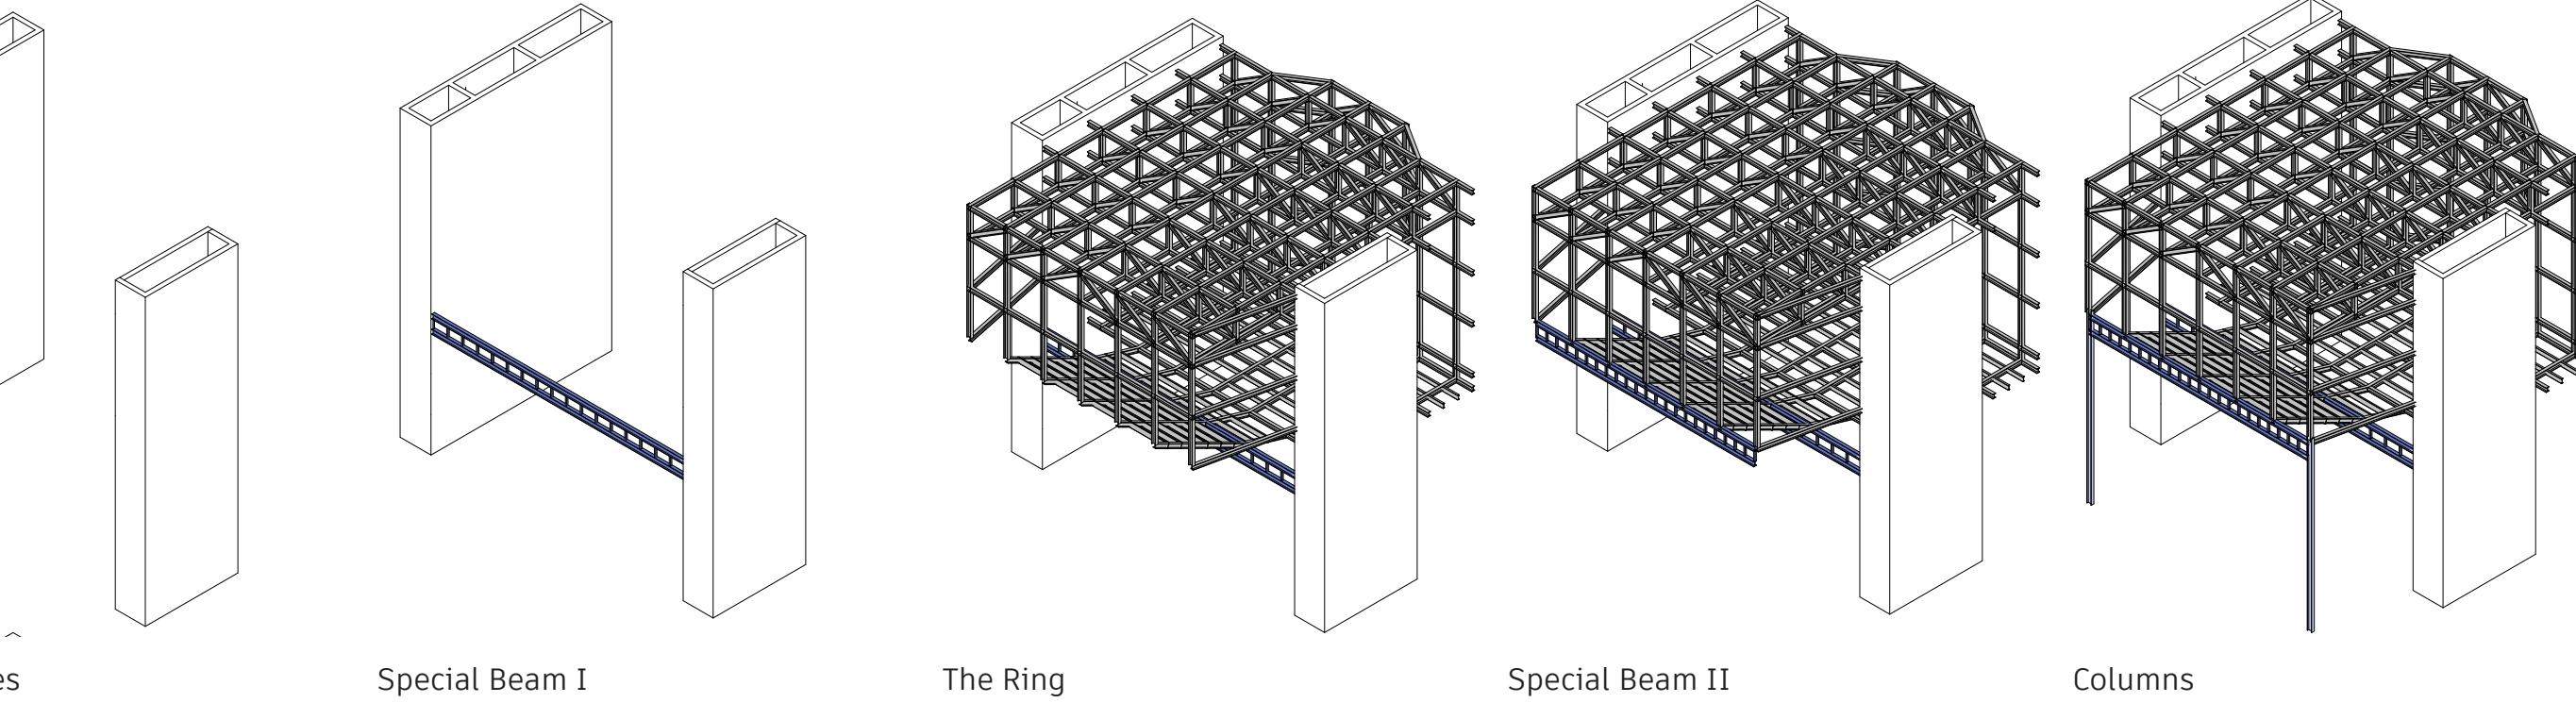

Structural Design

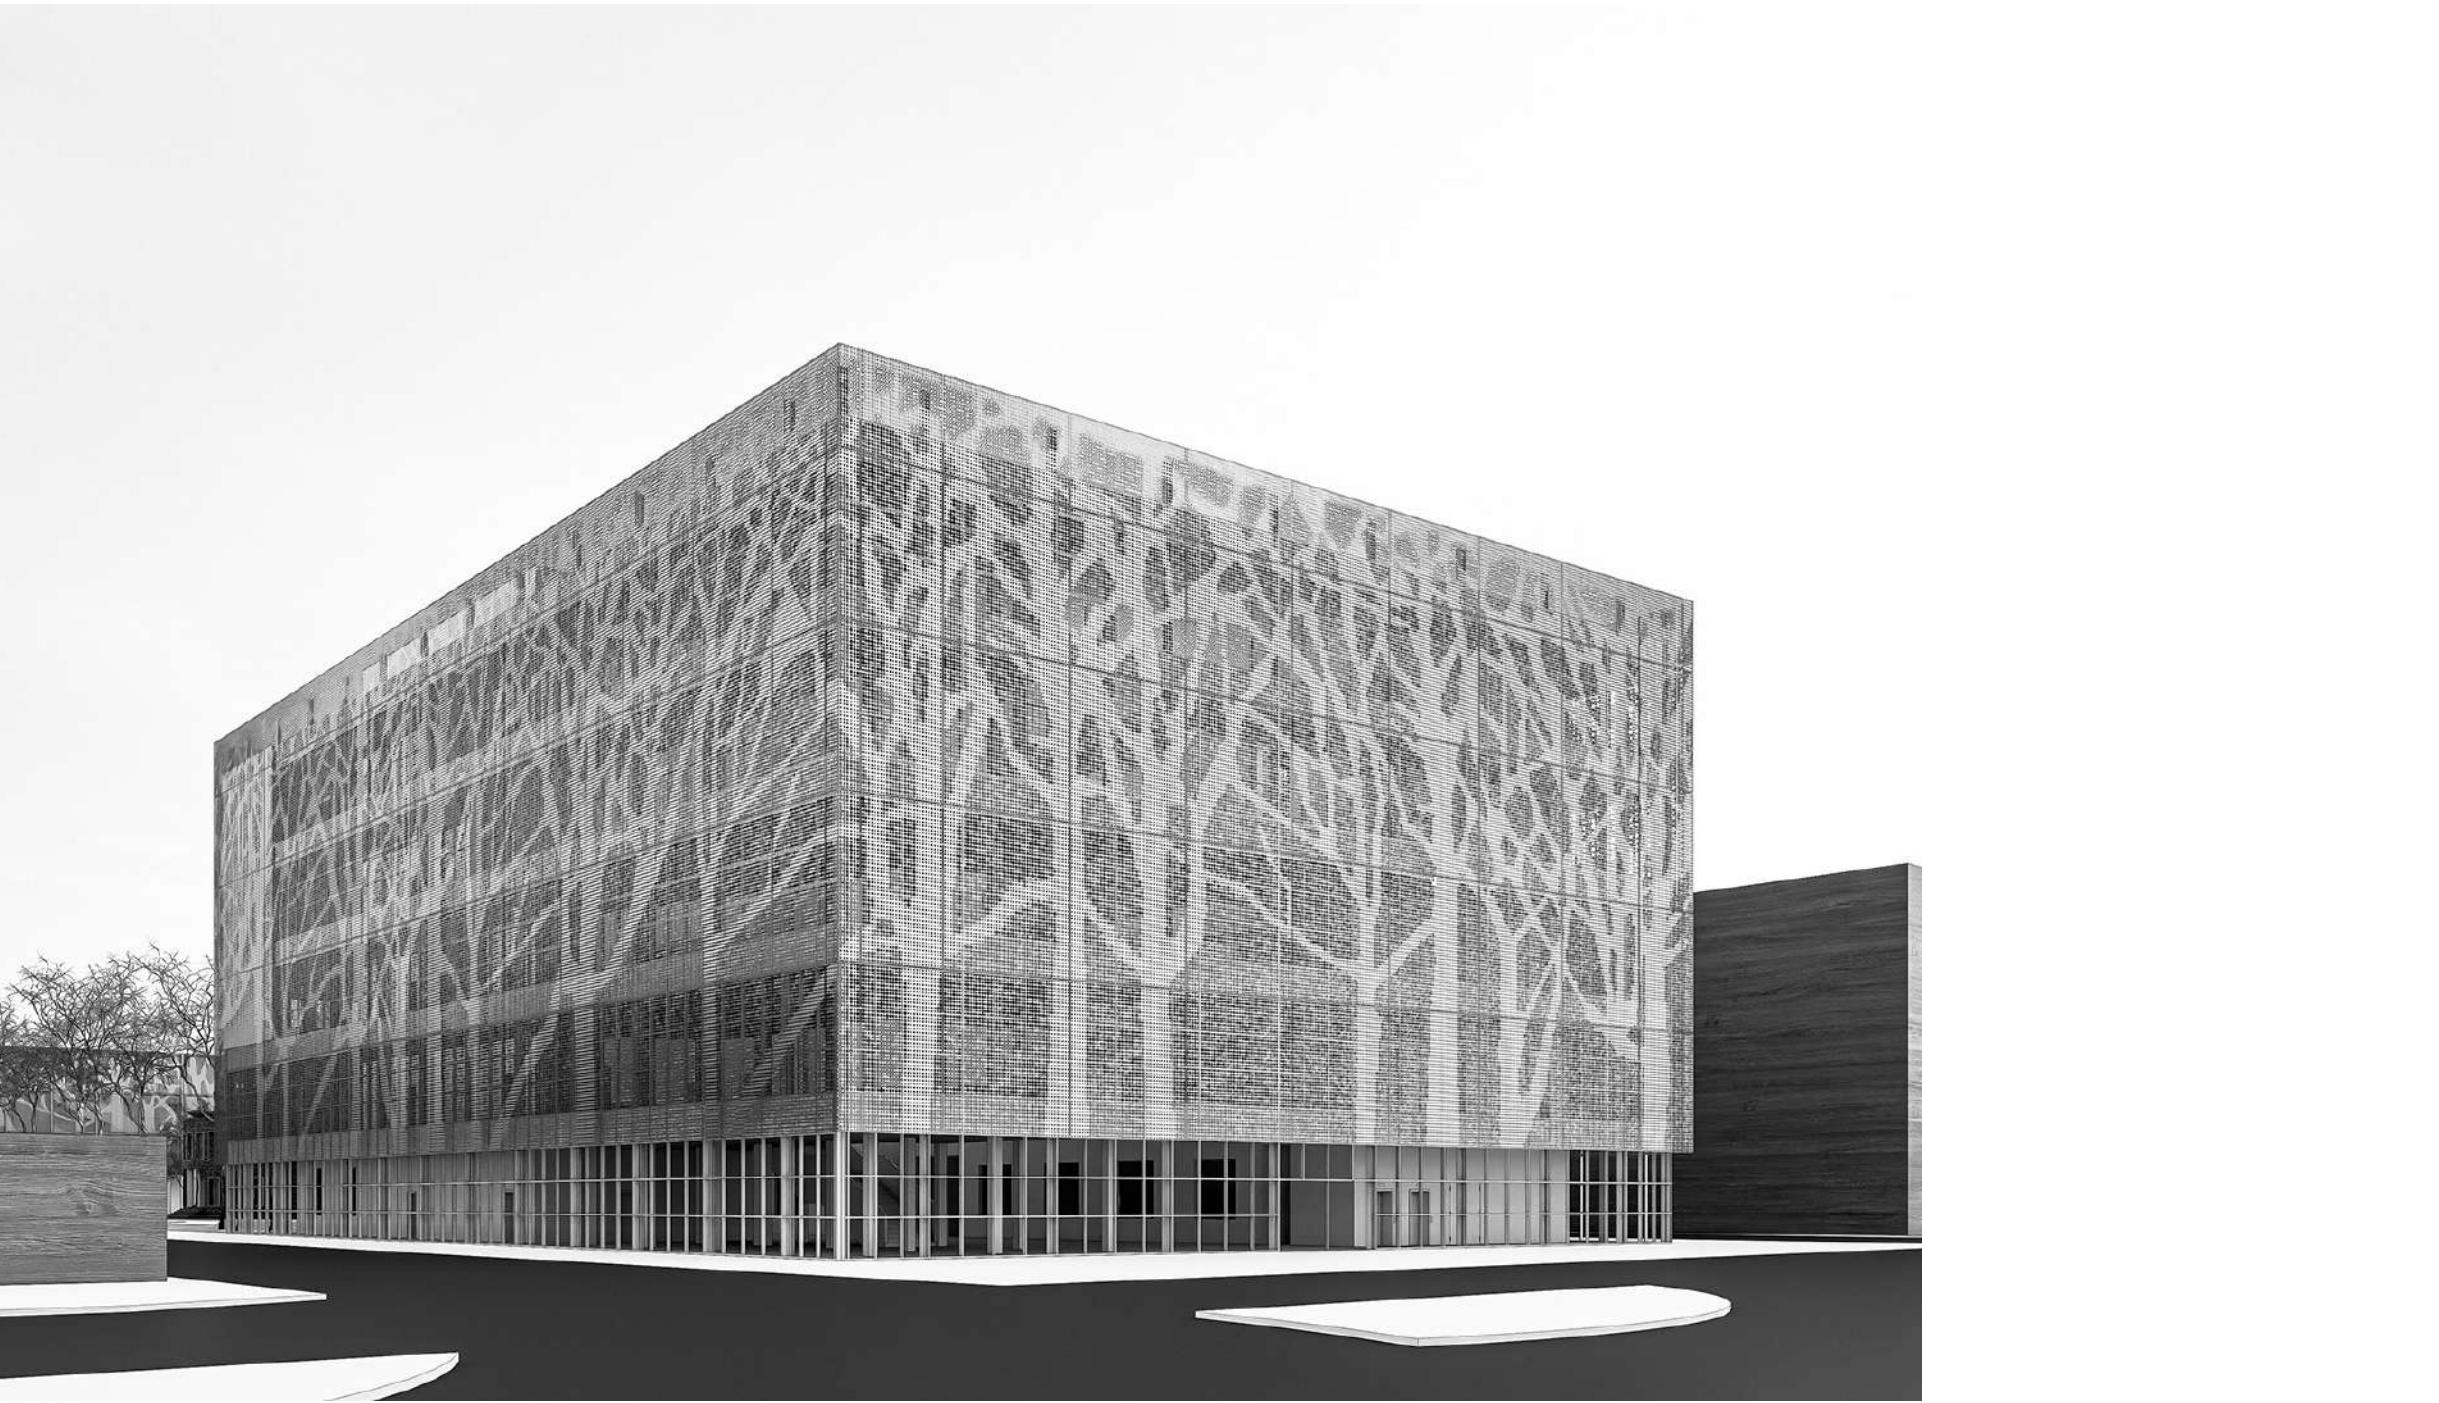

Politecnico di Milano

School of Architecture Urban Planning Construction Engineering  
Master of Science Architecture - Building Architecture 2023/2024  
Architectural Design Studio For Complex Constructions 1

Prof. Maria Grazia Folli, Prof. Aldo Nolli, Prof. Corrado Pecora  
Prof. Marco Imperadori

### TIMBER TALL BUILDING




TIMBER TALL BUILDING ZURICH SWITZERLAND




3 Hours Analysis



Urban Context

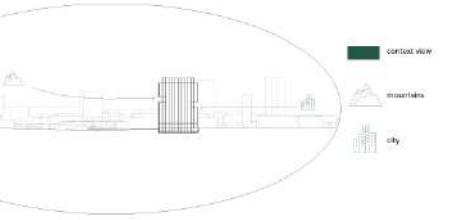


Functions

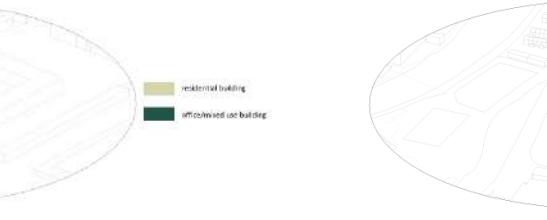

Barriers



Ground Floor Plan (+0.00)

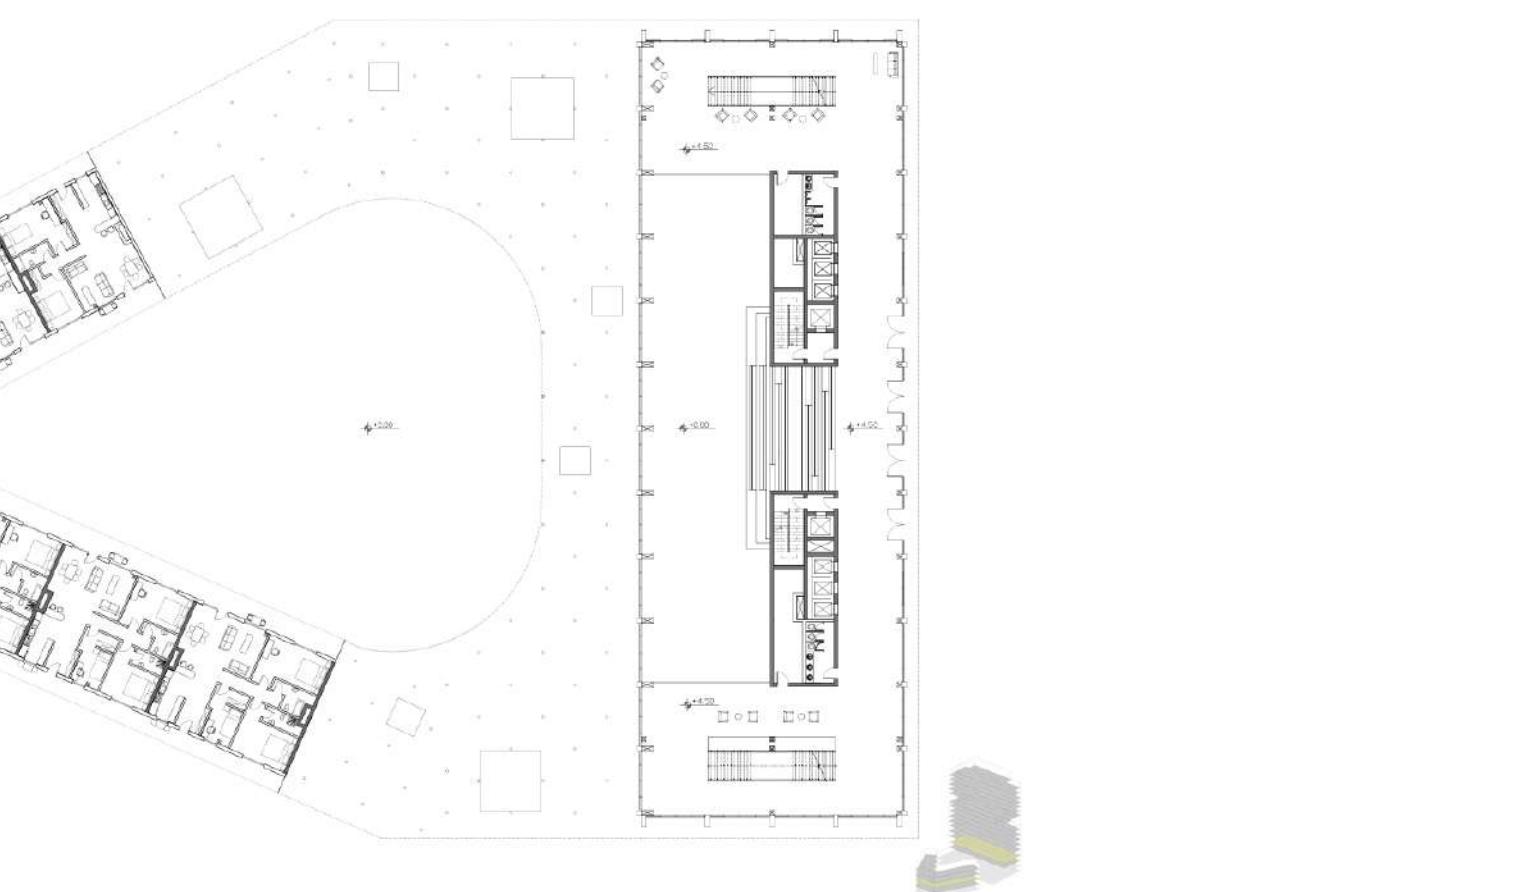



First Floor Plan (+4.50)



North Elevation




West Elevation

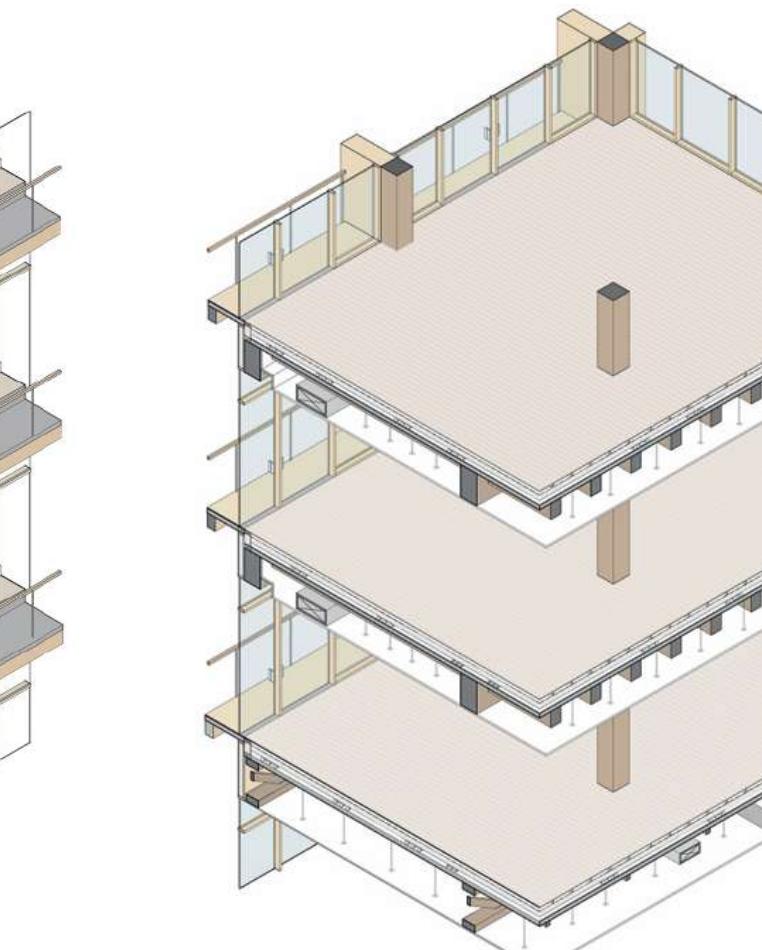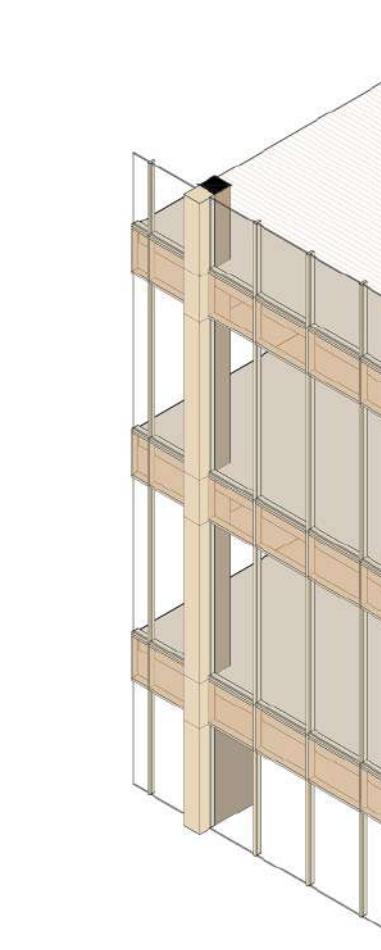





View From Special SemiOpen Through City

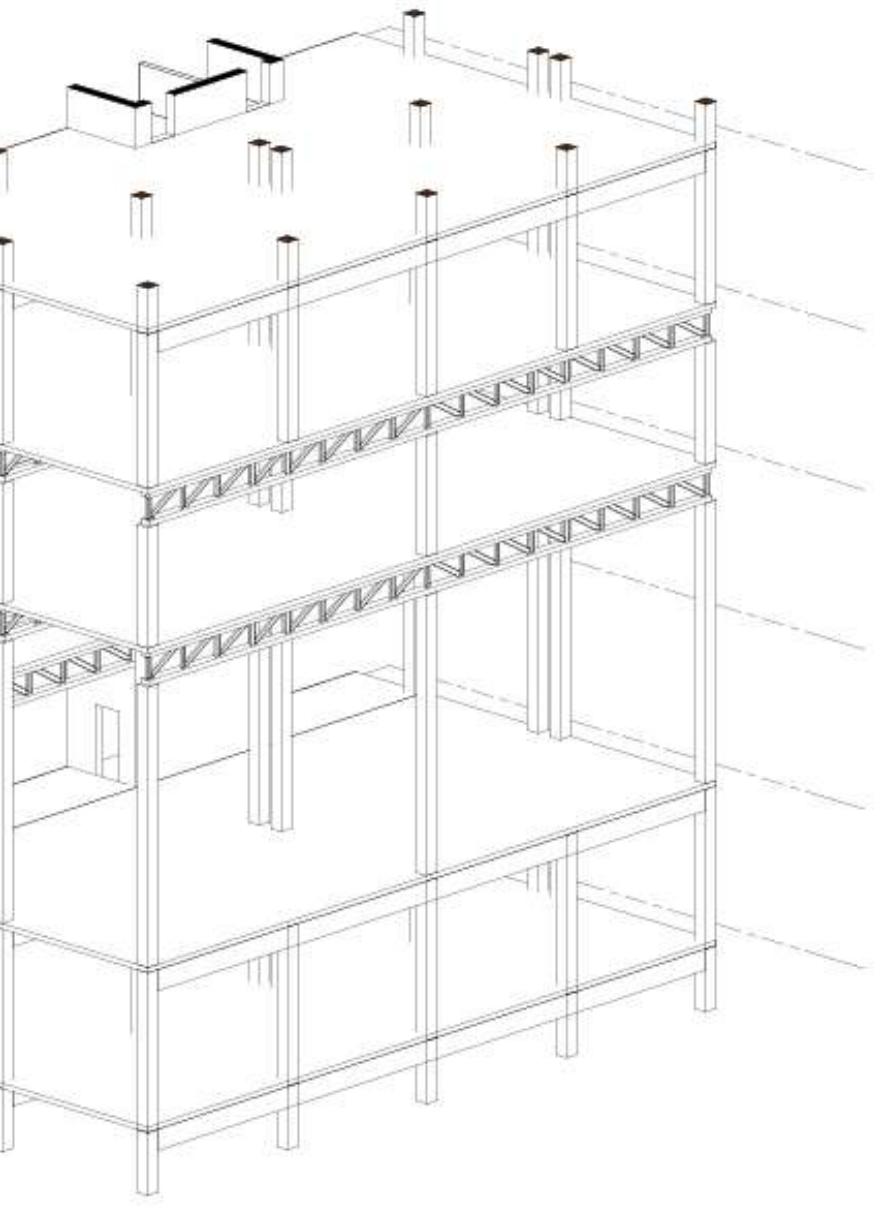

Structural Design of Special Opening

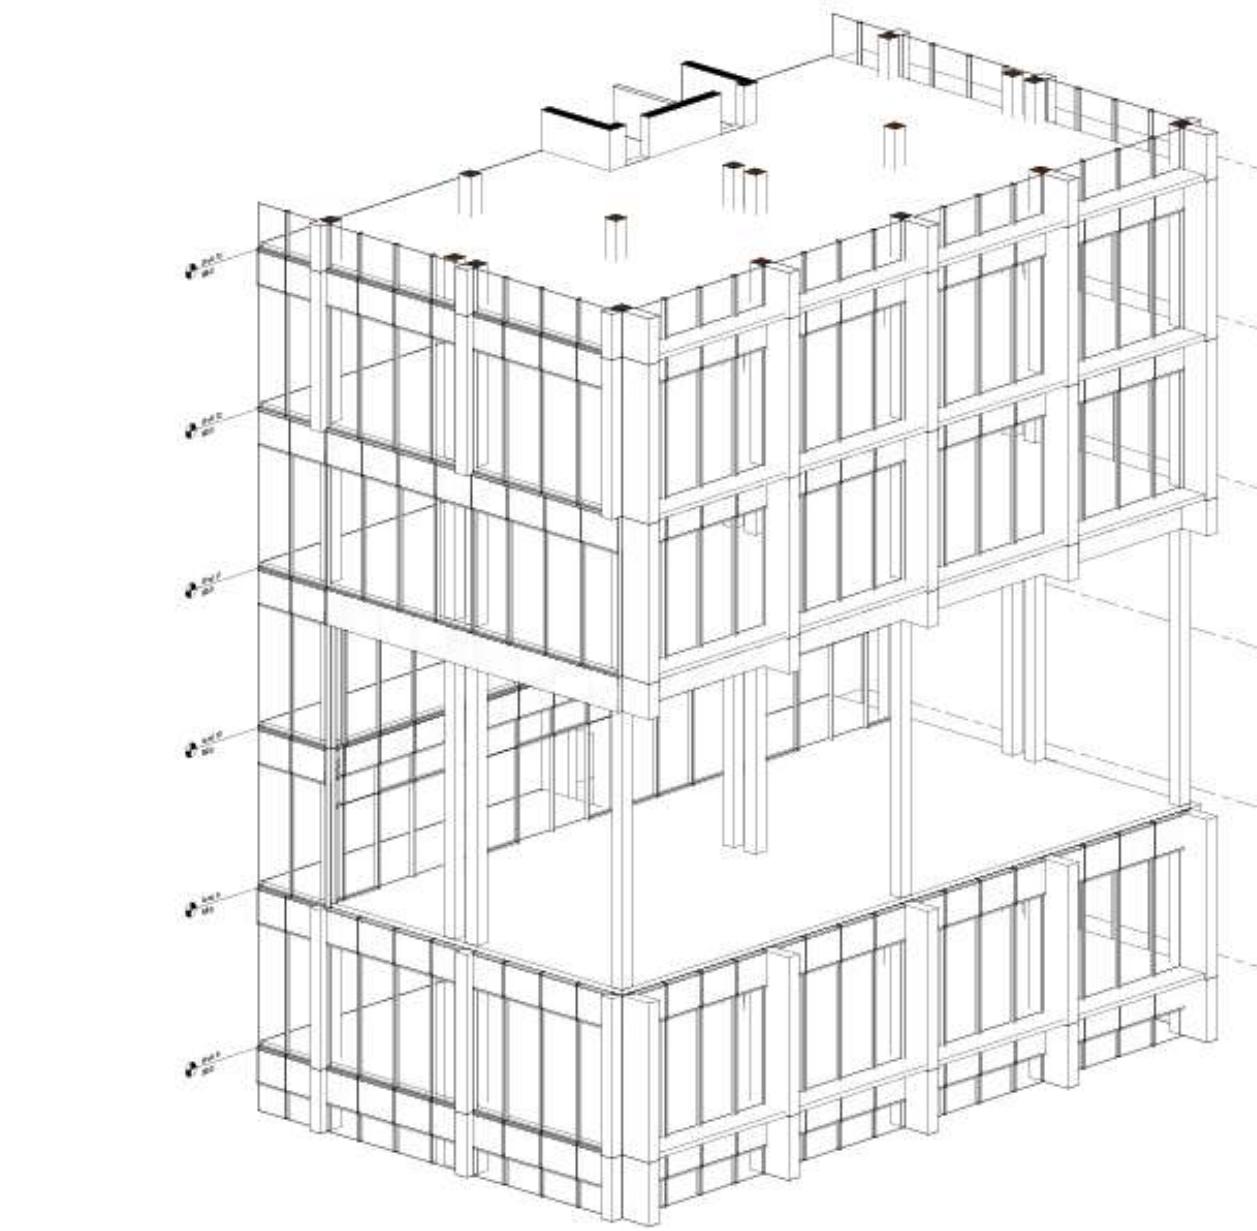

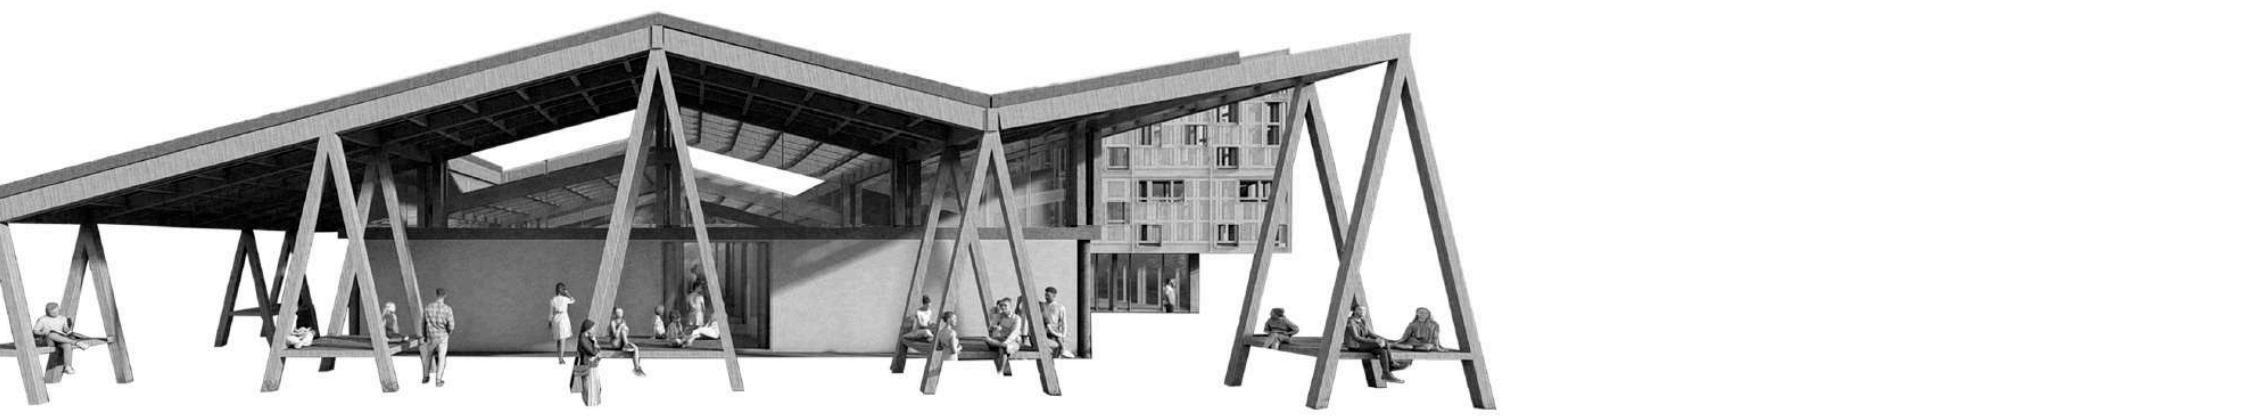



Politecnico di Milano

School of Architecture Urban Planning Construction Engineering  
Master of Science Architecture - Building Architecture 2023/2024  
Sustainable Architecture Construction Studio


Prof. Gian Luca Brunetti, Prof. Giacomo Boffi, Prof. Marco Scaioni

CINIFABRIQUE


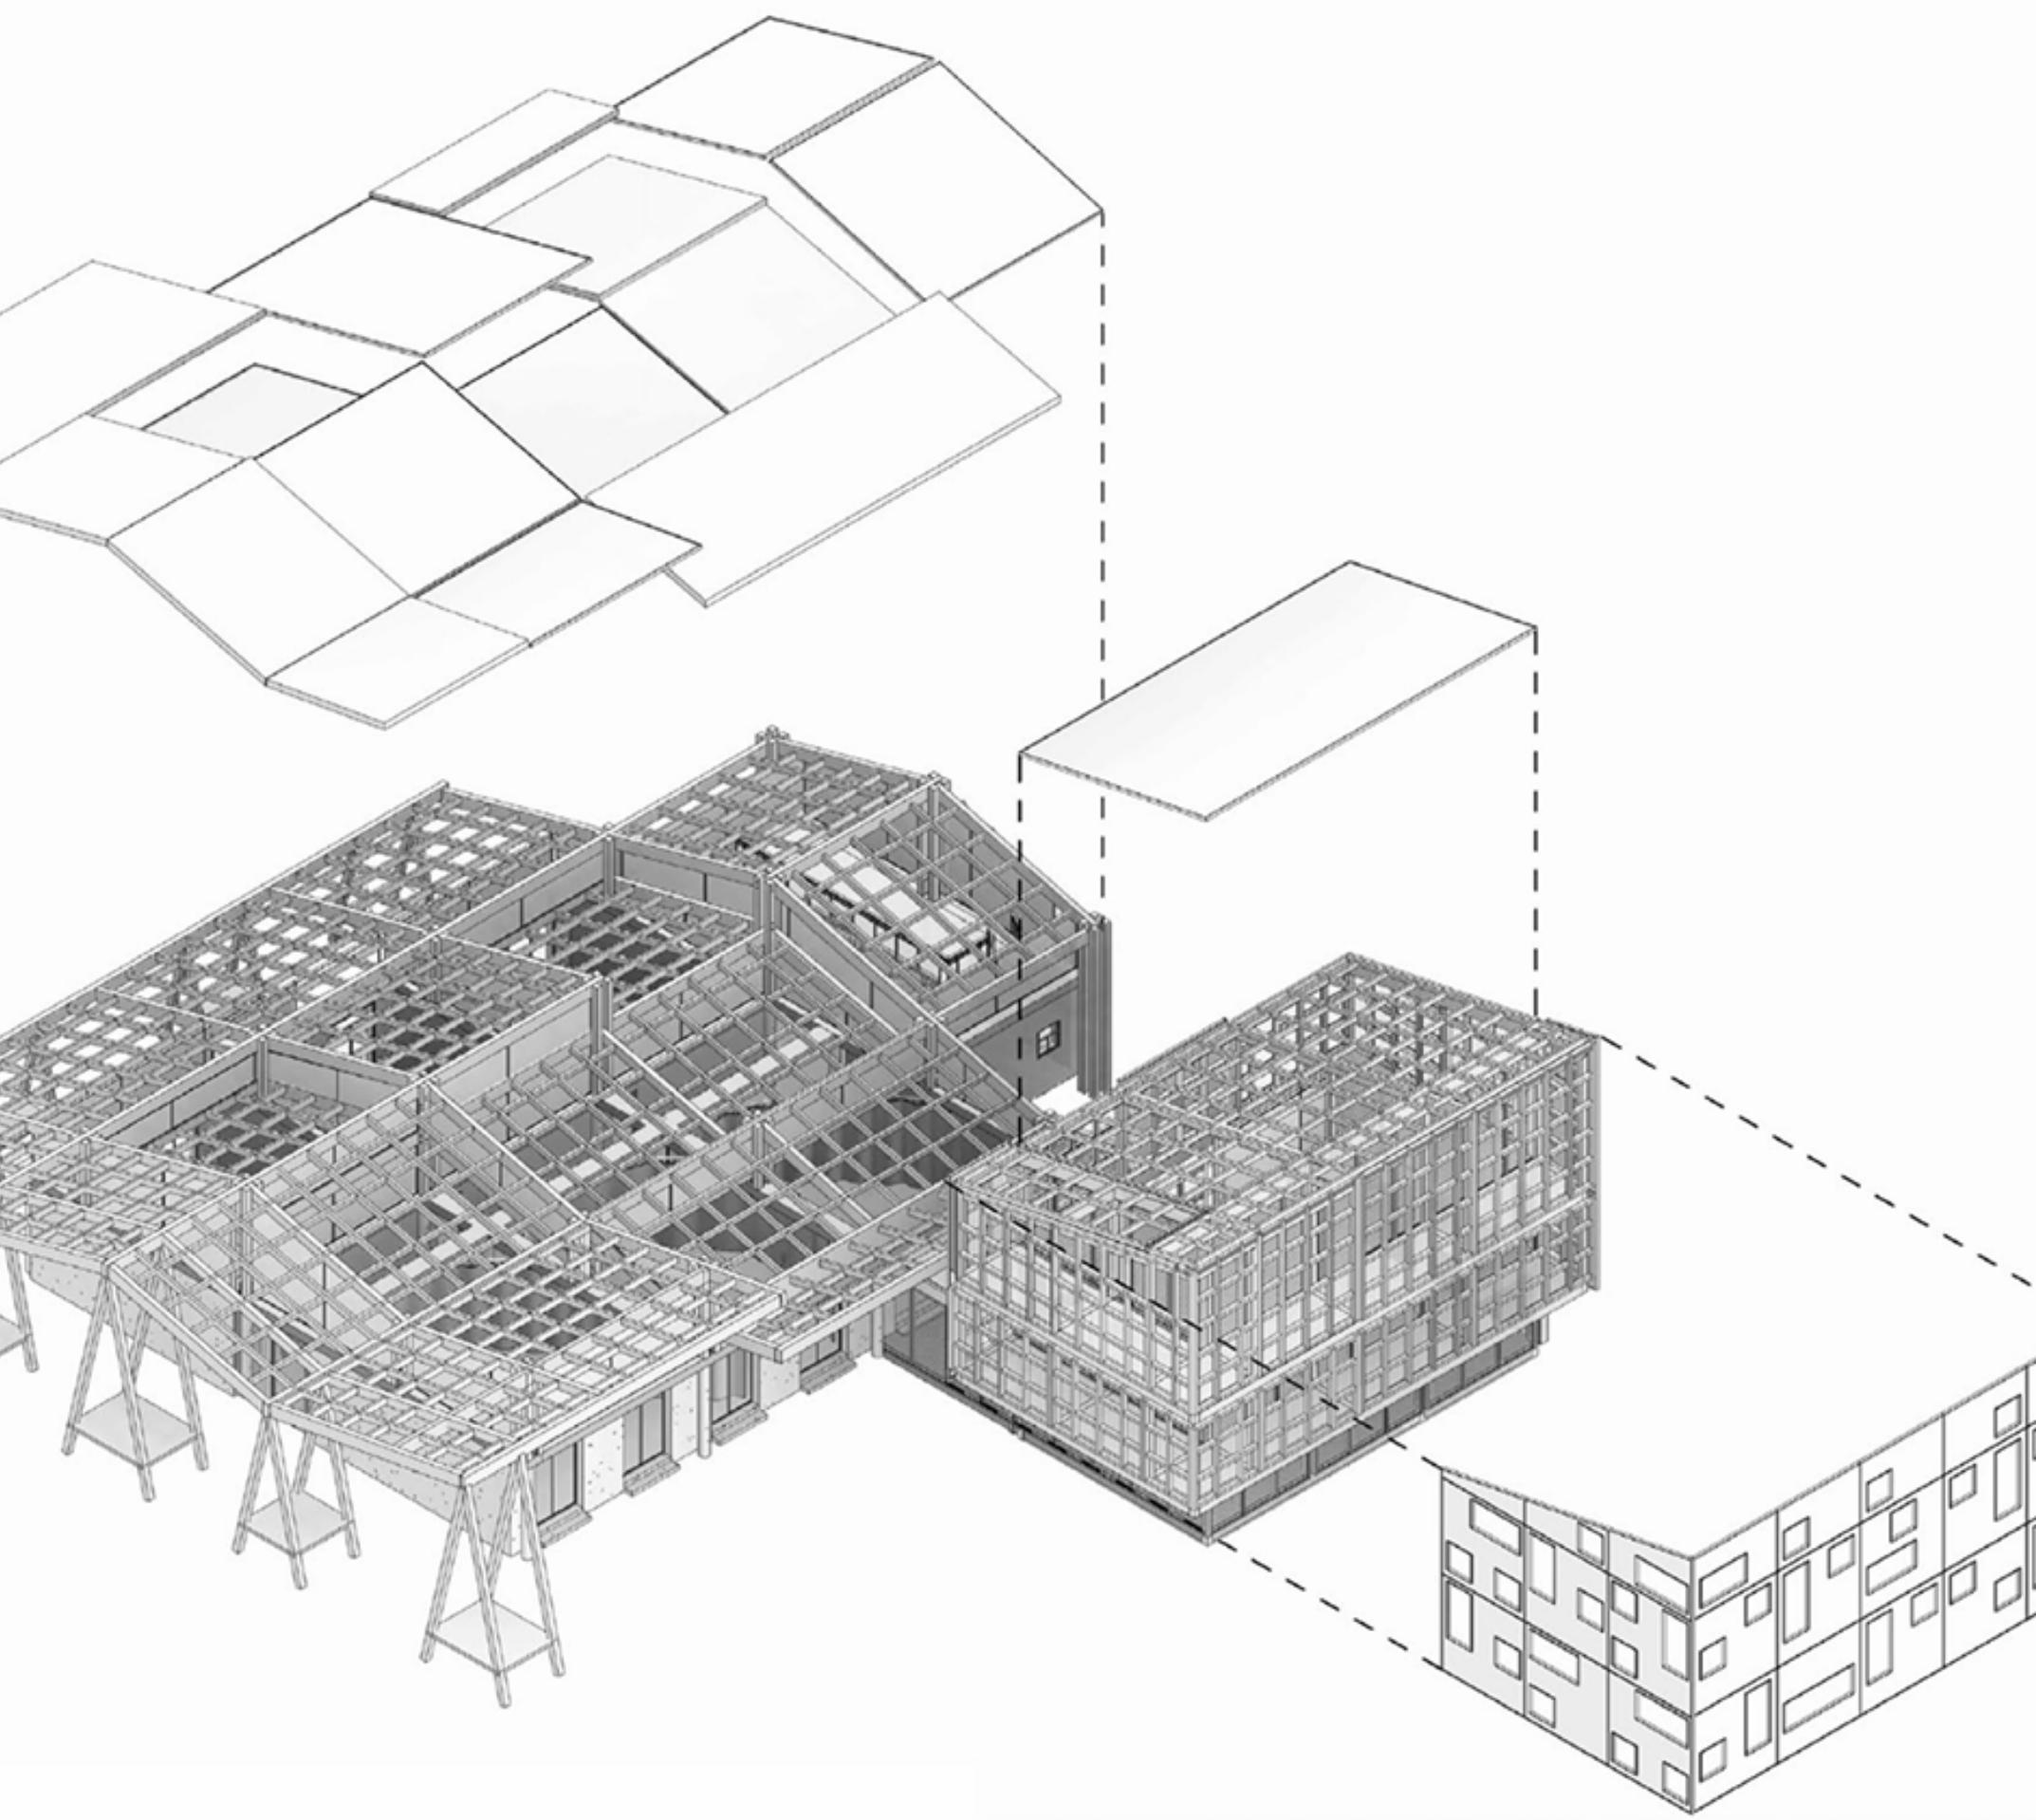


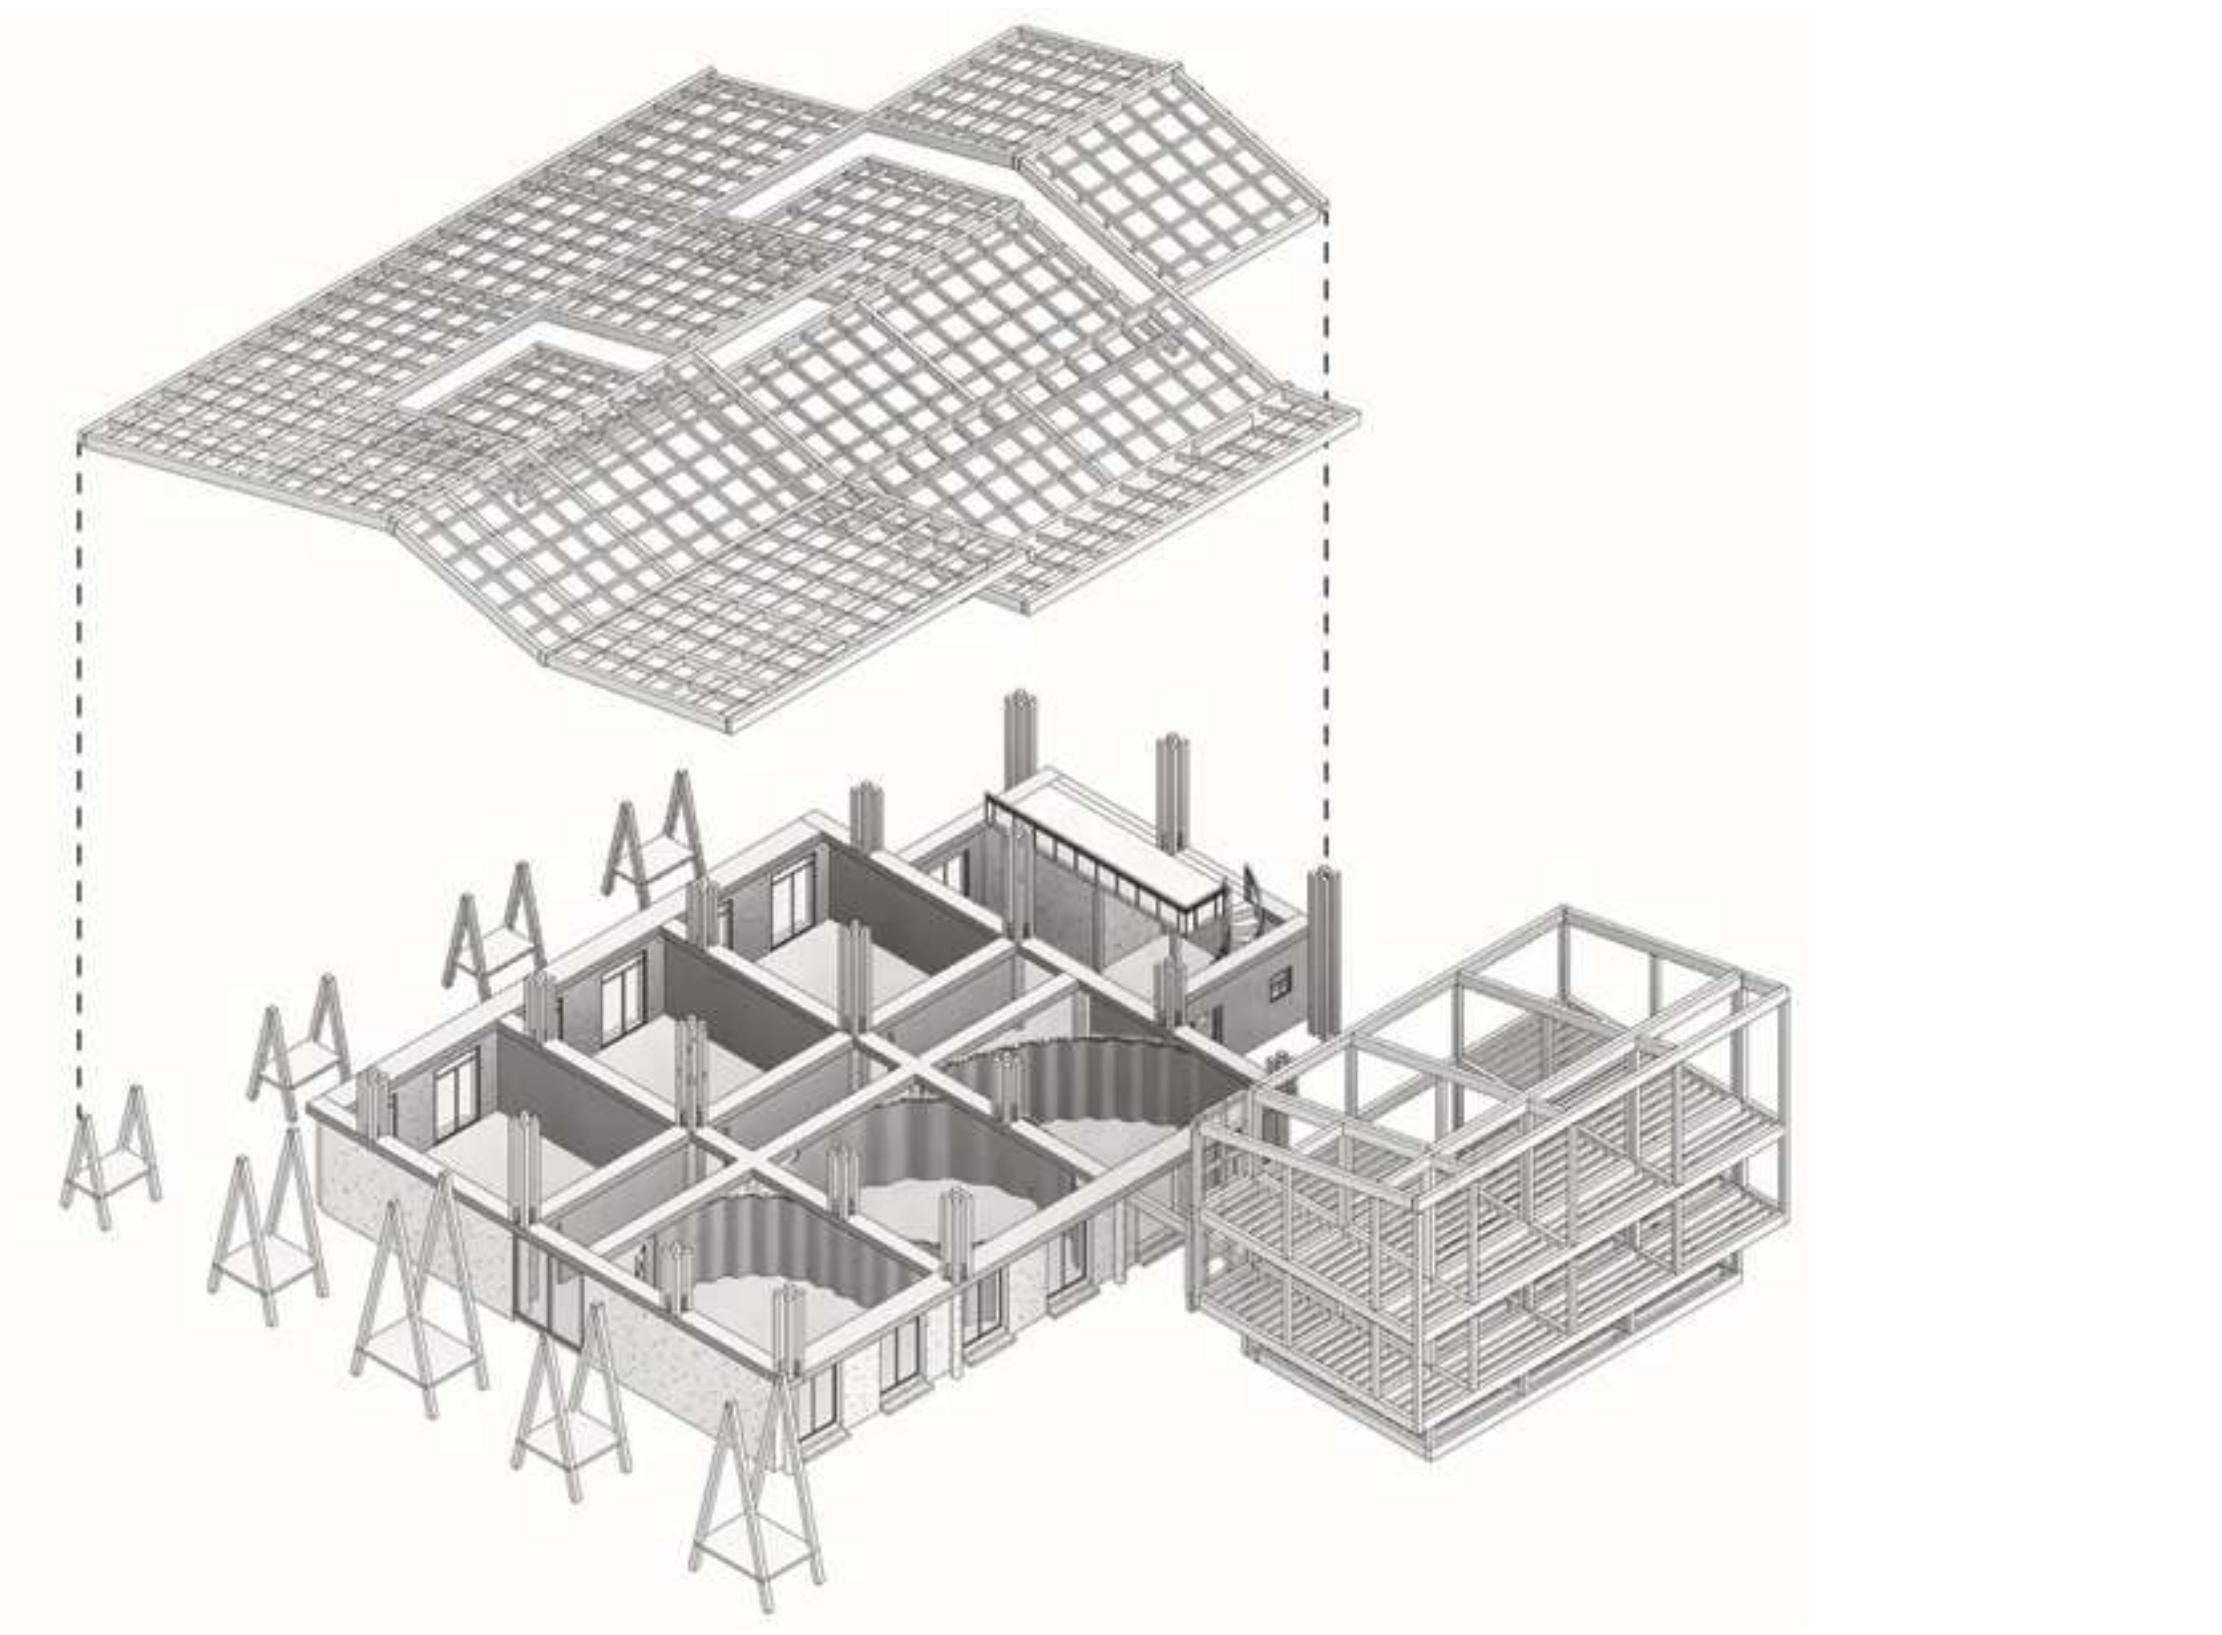


Existing Building and Additional Building awith New Roof Design in Timber Materiality

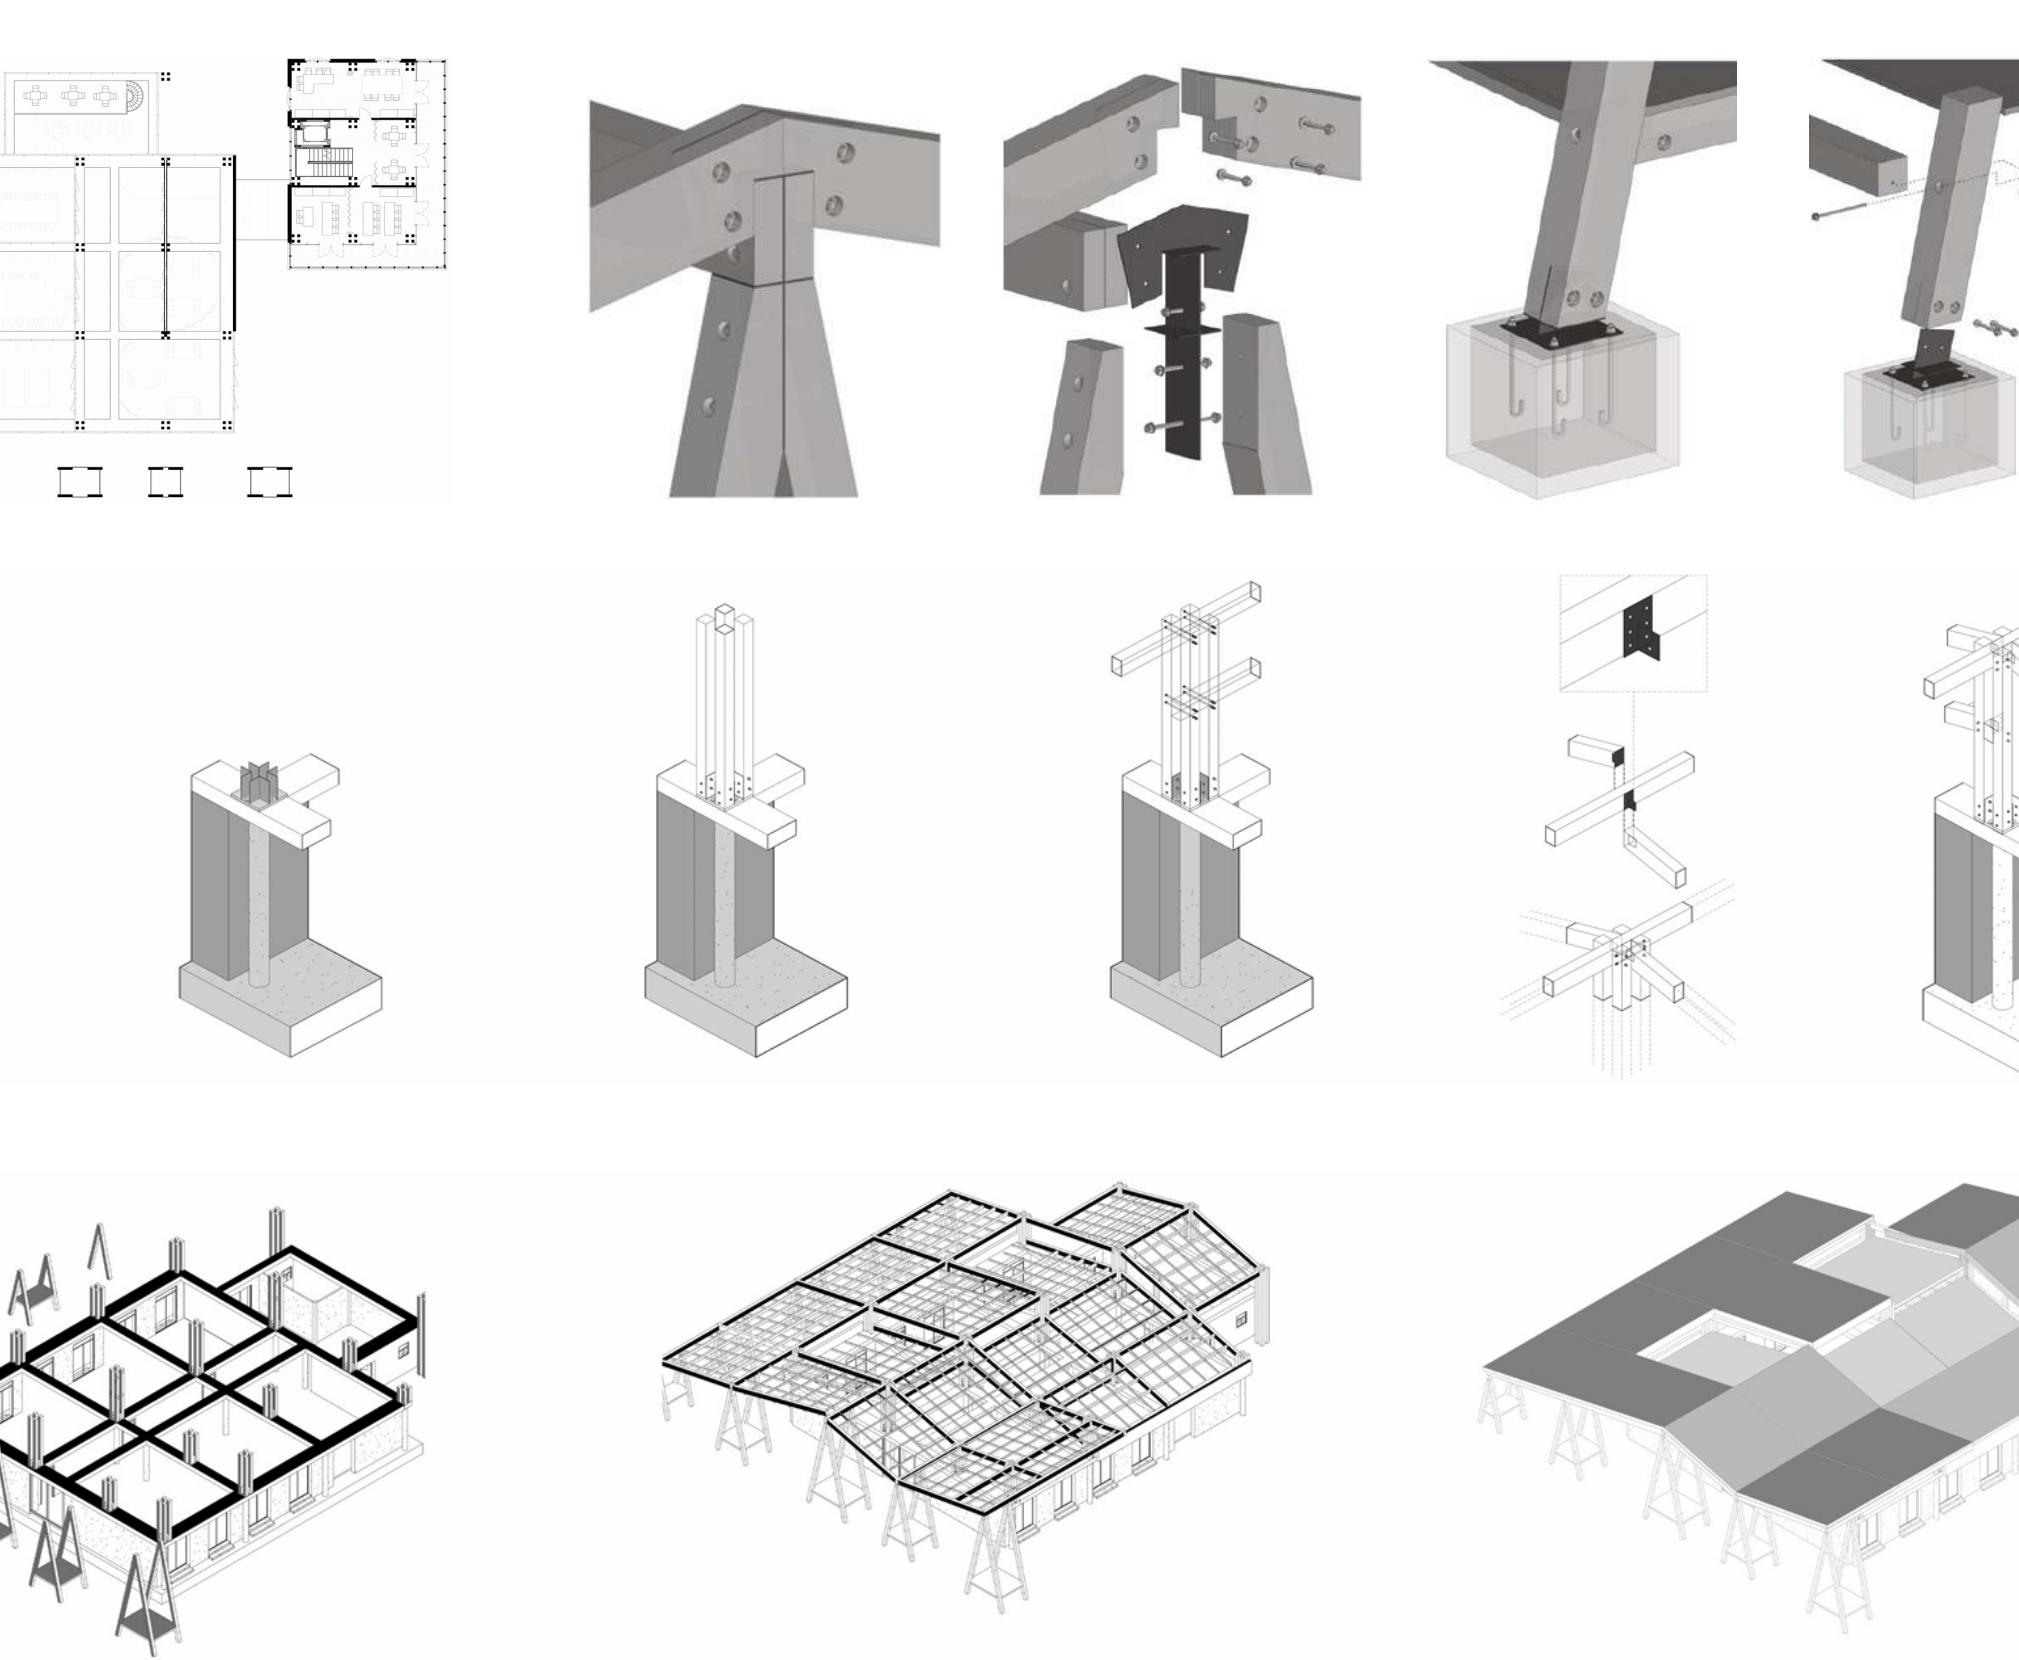

Structural Details and Applications

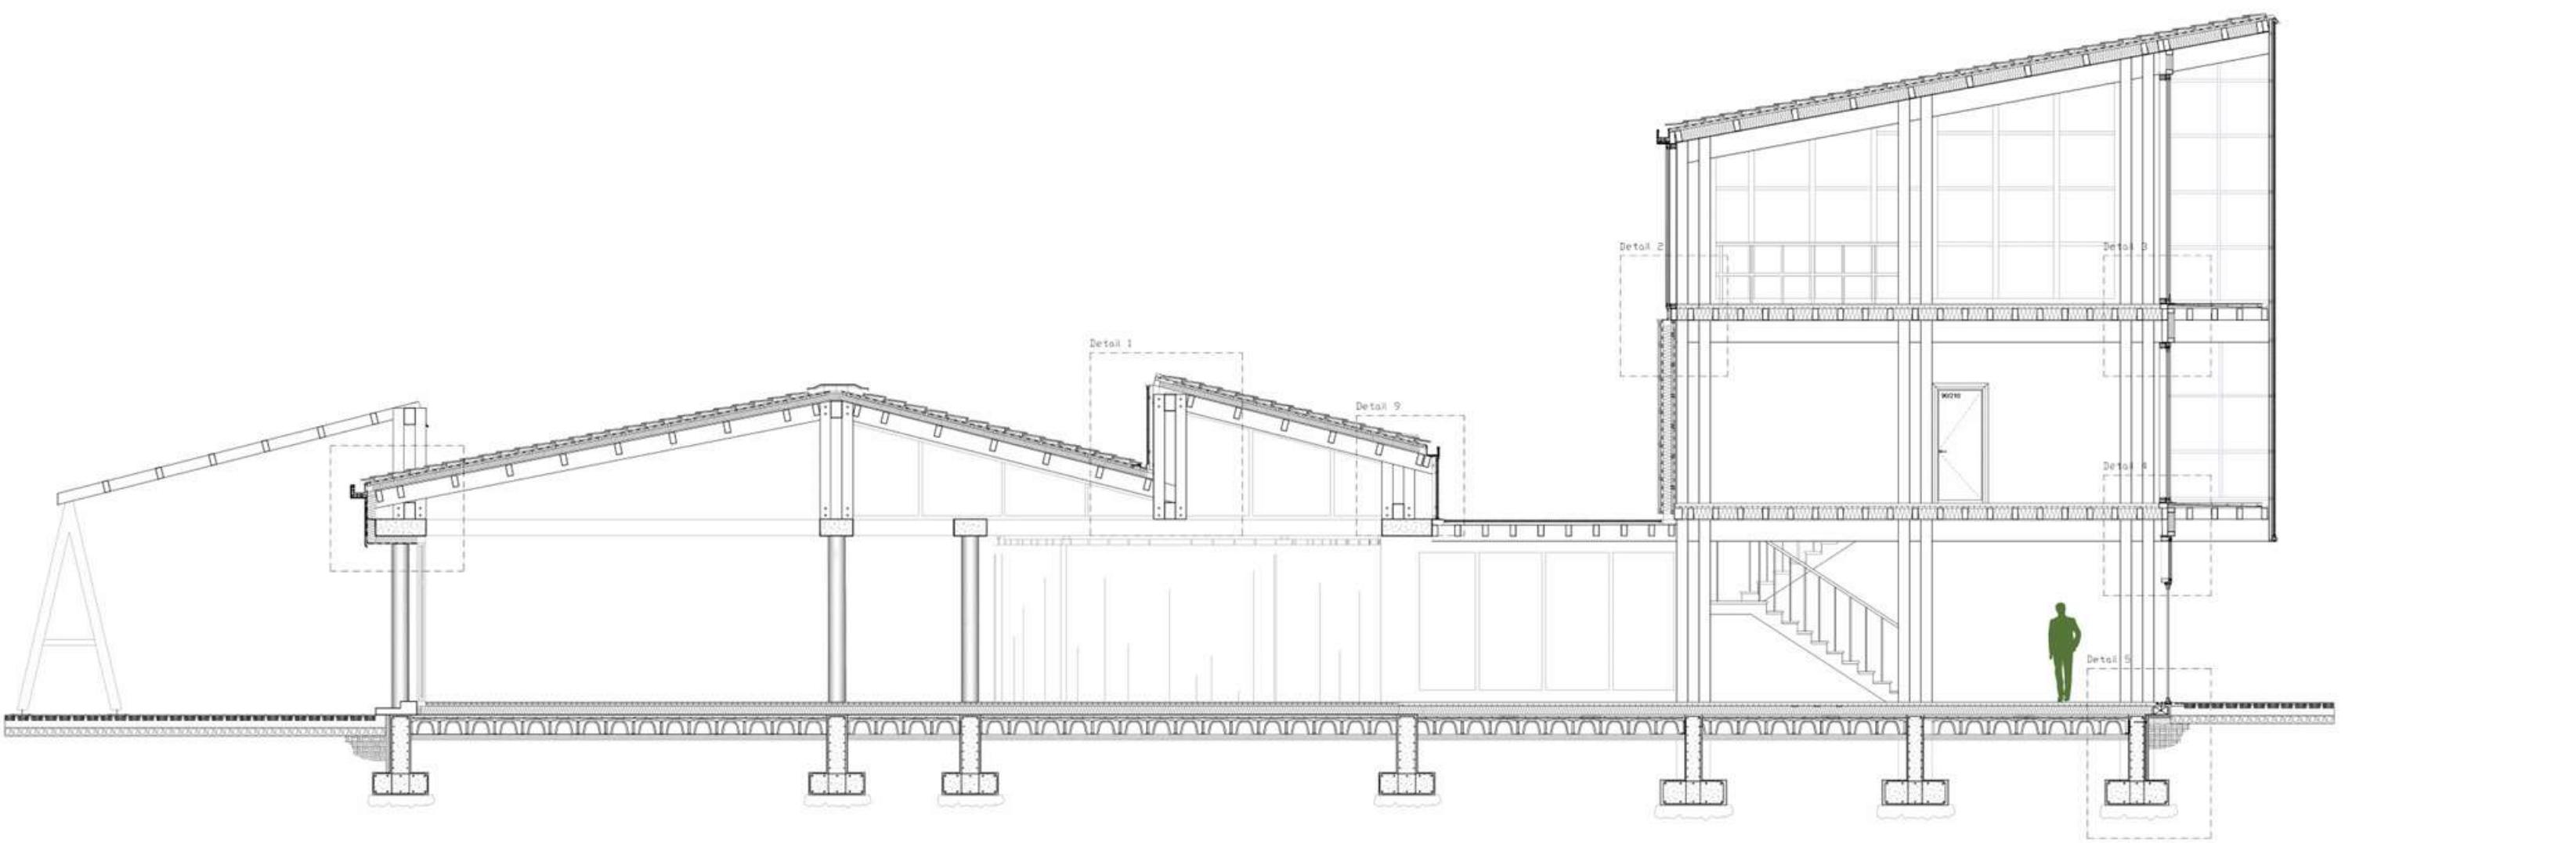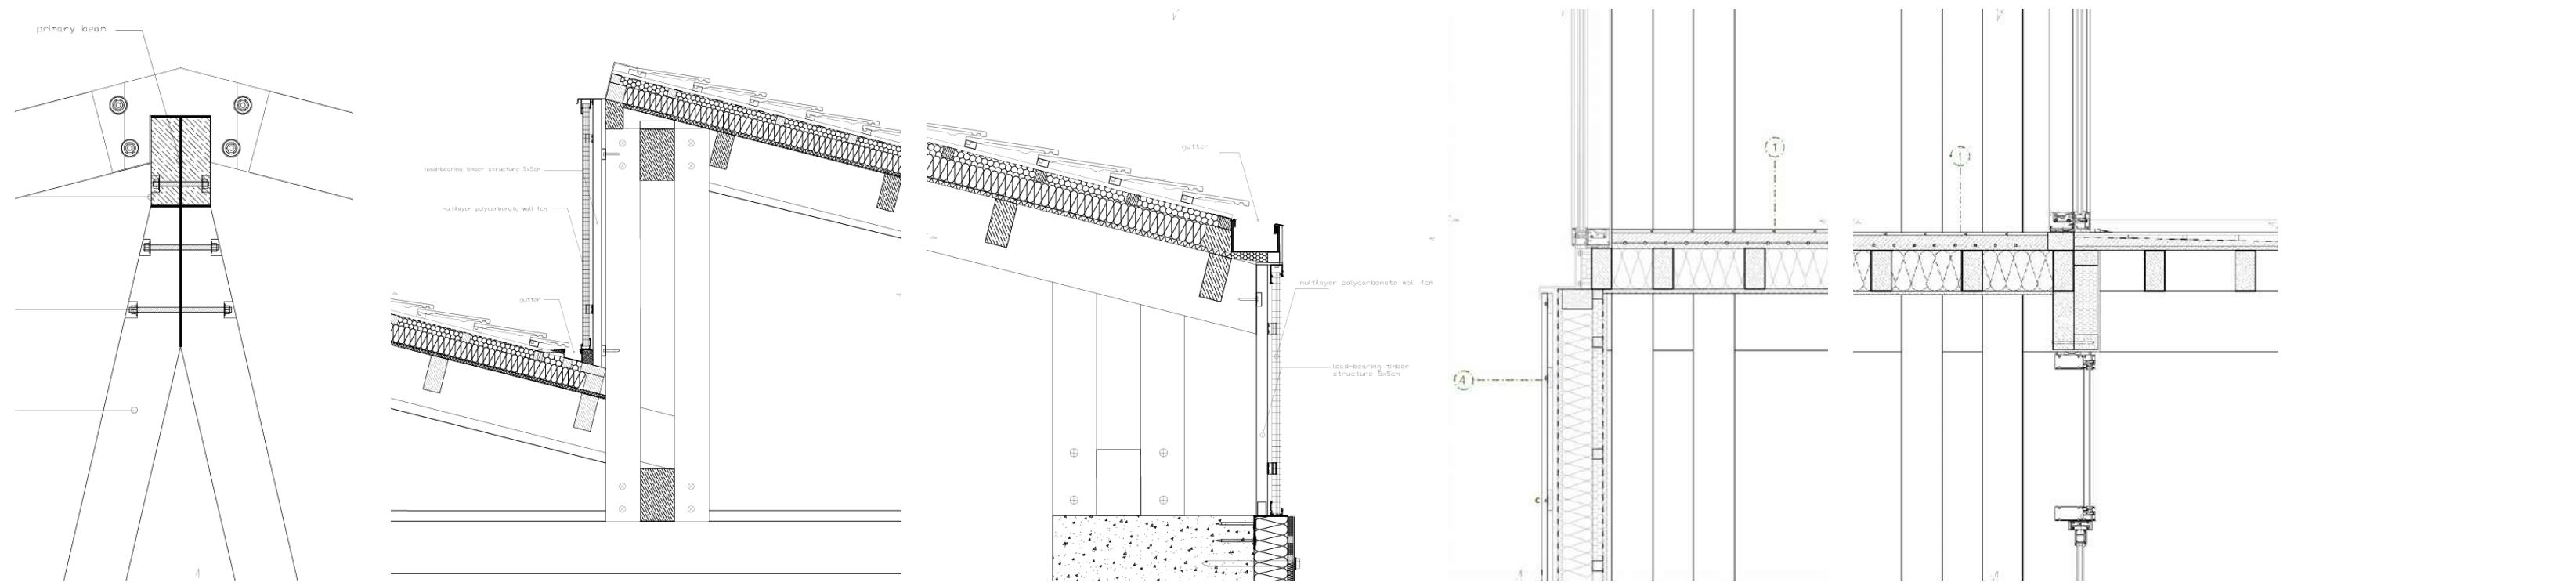

1:50 Section and 1:20 Node Section Details

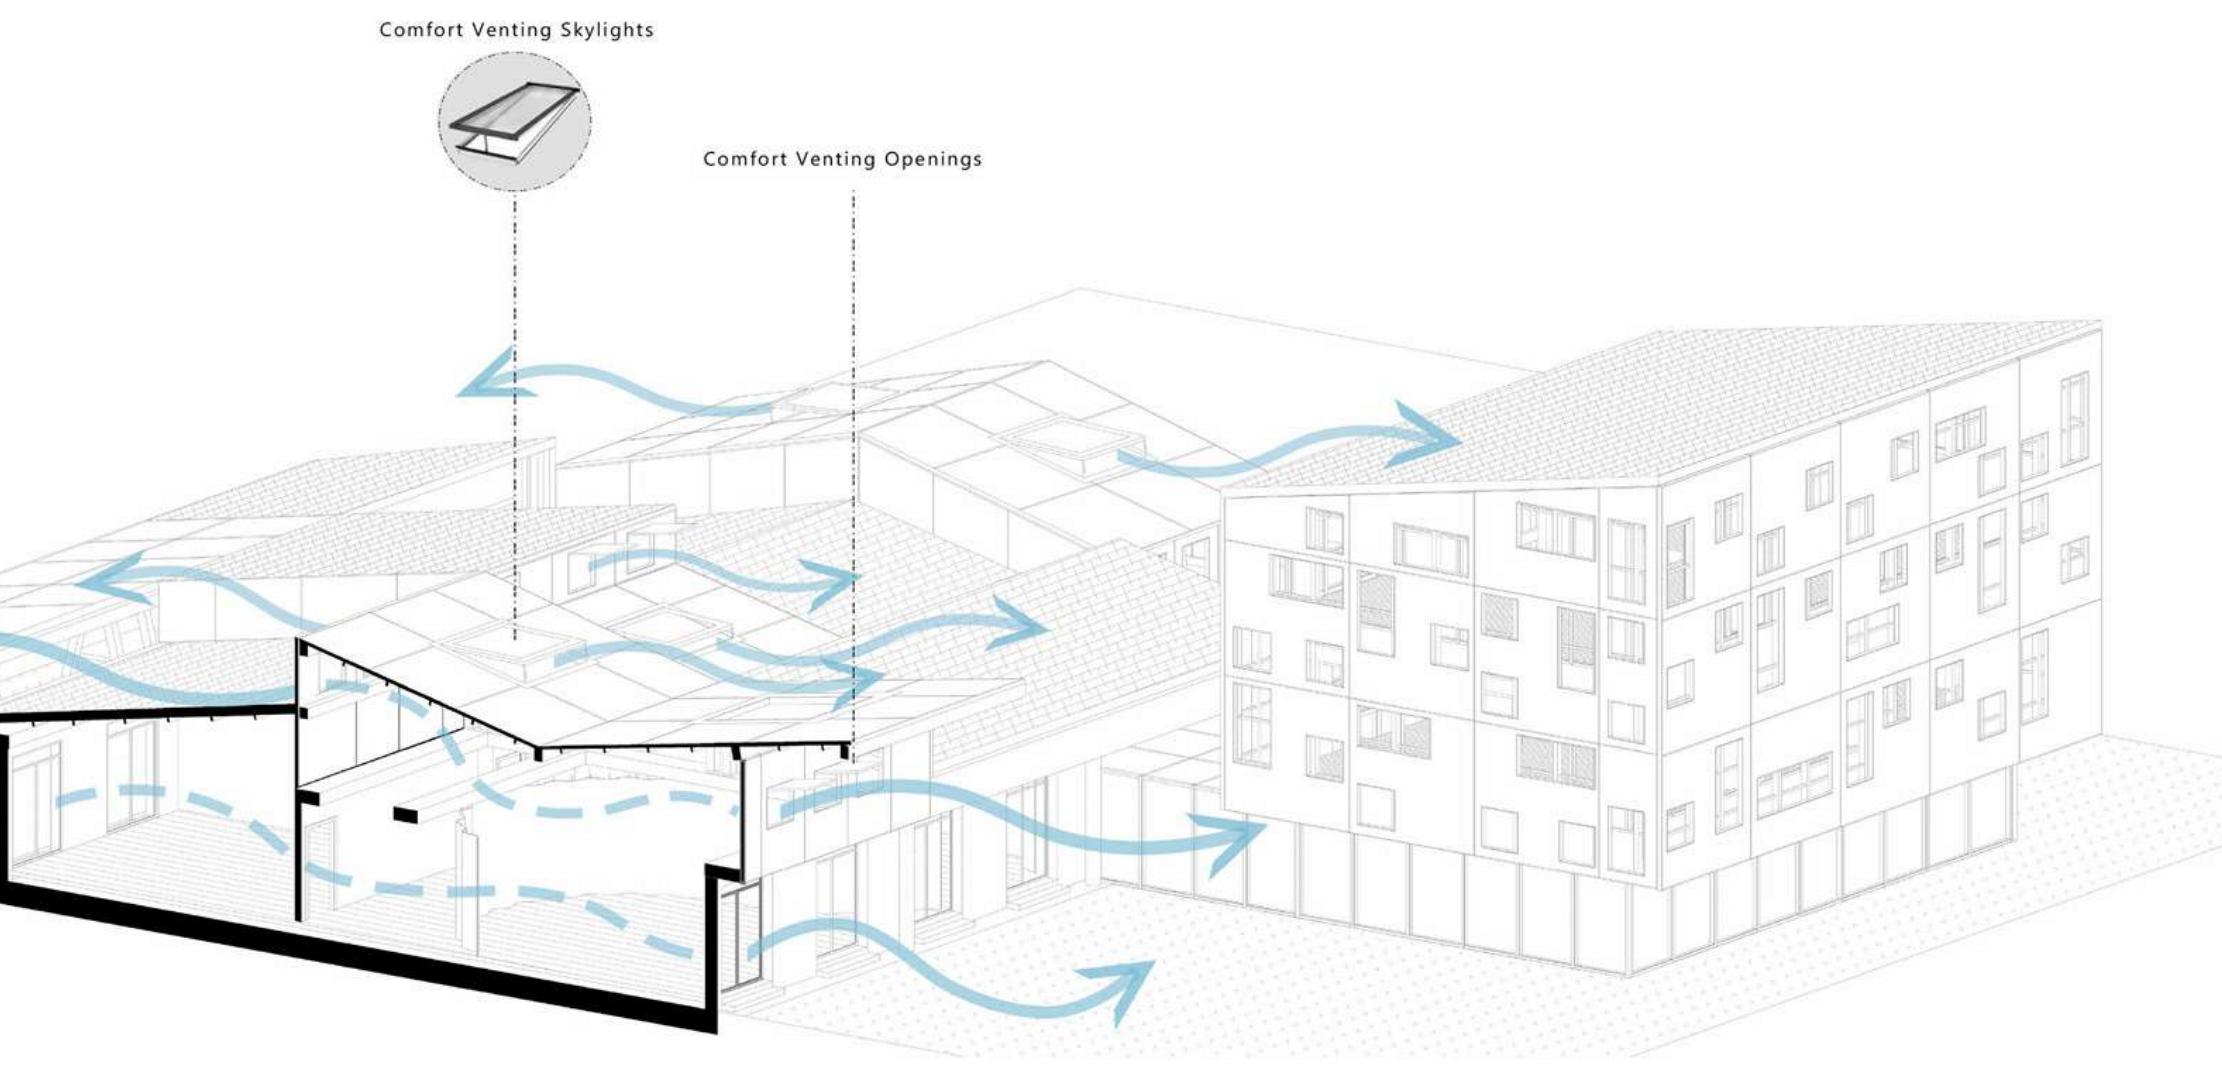

Axonometric Section with Ventilation Diagram

